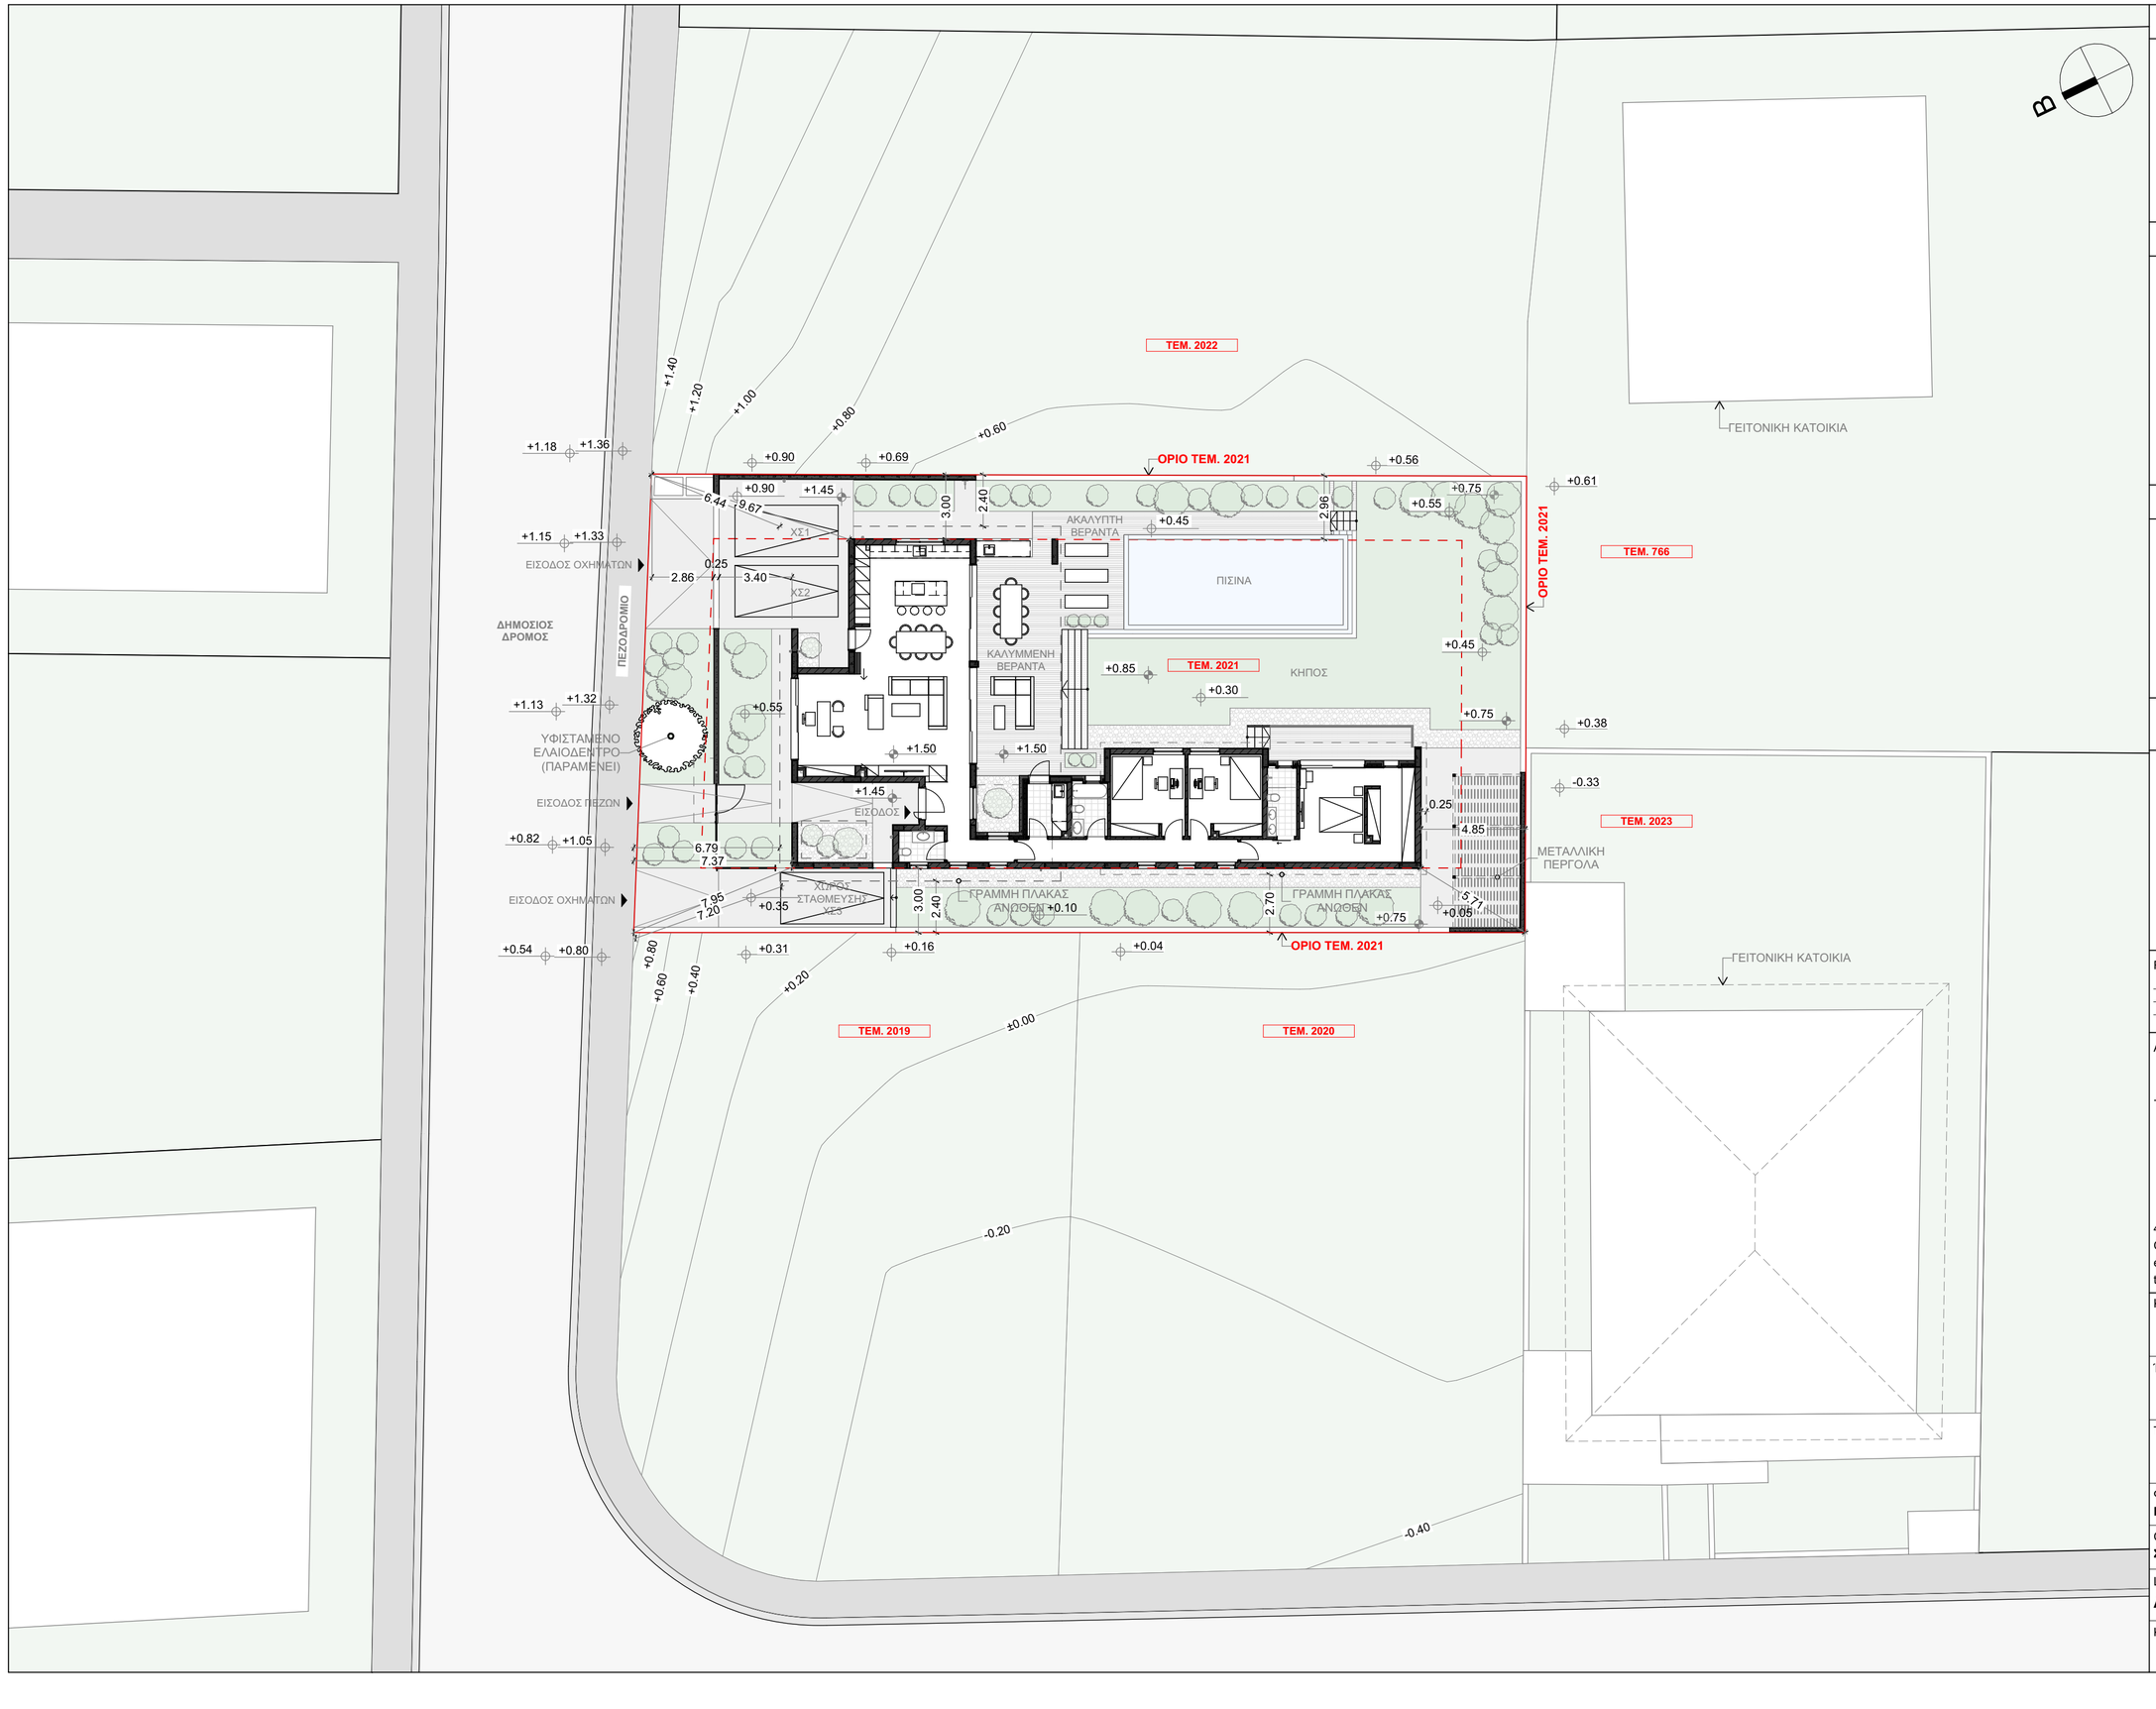


Υπόμνημα Υψομέτρων

— ±000.00 —	ΥΦΙΣΤΑΜΕΝΕΣ ΙΣΟΫΨΕΙΣ ΓΡΑΜΜΕΣ
±000.00	ΥΦΙΣΤΑΜΕΝΑ ΥΨΟΜΕΤΡΑ
±000.00	ΠΡΟΤΕΙΝΟΜΕΝΑ ΥΨΟΜΕΤΡΑ

±0.00μ. = +214μ. (ΠΡΑΓΜΑΤΙΚΟ ΥΨΟΜΕΤΡΟ)

Υπόμνημα Υλικών

1	Μπετόν Σανιδωτό
2	Οπτοπλινθοδομή / Σοβάς
3	Μπετόν / Σοβάς
4	Επένδυση Alucobond
5	Πλέγμα
6	Μεταλλική Πέργολα

Στοιχεία Τεμαχίου

ΤΜΗΜΑ/ΑΡ. ΕΓΓΡΑΦΗΣ: 6/2100
ΦΥΛΛΟ/ΣΧΕΔΙΟ: 30/23Ε2
ΑΡ. ΤΕΜΑΧΙΟΥ: 2021
ΔΗΜΟΣ: ΛΑΤΣΙΩΝ
ΕΝΟΡΙΑ: ΑΓΙΟΣ ΓΕΩΡΓΙΟΣ
ΠΟΛΕΟΔΟΜΙΚΗ ΖΩΝΗ: Κα6

ΕΓΓΕΓΡΑΜΜΕΝΟ ΩΣ ΟΙΚΟΠΕΔΟ

ΣΤΟΙΧΕΙΑ ΕΡΓΟΥ: ΙΣΟΓΕΙΑ ΚΑΤΟΙΚΙΑ
ΔΟΜΗΣΙΜΟ ΕΜΒΑΔΟΝ: 190.00τ.μ.

ΕΝΤΟΛΗ 2/2020
ΠΟΛΕΟΔΟΜΙΚΗ ΑΔΕΙΑ

ΕΥΣΤΑΘΙΟΣ ΛΕΥΚΑΤΗΣ
ΑΡΧΙΤΕΚΤΟΝΑΣ
Α.Μ.ΕΤΕΚ: Α173321

Revision History

RevID	Comment	Date

Αρχιτέκτονας / Architect

STATHIS LEFKATIS ARCHITECTURE

4, KOURIOU STREET, LATSIA, NICOSIA
CYPRUS, 2220
e-mail: efstathios.lefkatis@gmail.com
tel: 99841485

Κύριος Έργου / Client

ΑΝΤΡΕΑΣ & ΜΑΡΙΑ

Έργο / Project Name

ΙΣΟΓΕΙΑ ΚΑΤΟΙΚΙΑ


Τίτλος Σχεδίου / Drawing Name

ΧΩΡΟΤΑΞΙΚΟ

Φάση / Design Phase	Μελέτη / Study
ΠΟΛΕΟΔΟΜΙΚΗ ΑΔΕΙΑ	**ΑΡΧΙΤΕΚΤΟΝΙΚΗ**
Checked by	Ημερομηνία / Date
ΣΤΑΘΗΣ ΛΕΥΚΑΤΗΣ	**19/03/2026**
Layout ID	Revision
A1.1	

Κλίμακα Σχεδίου / Drawing Scale

1:200 @ A2

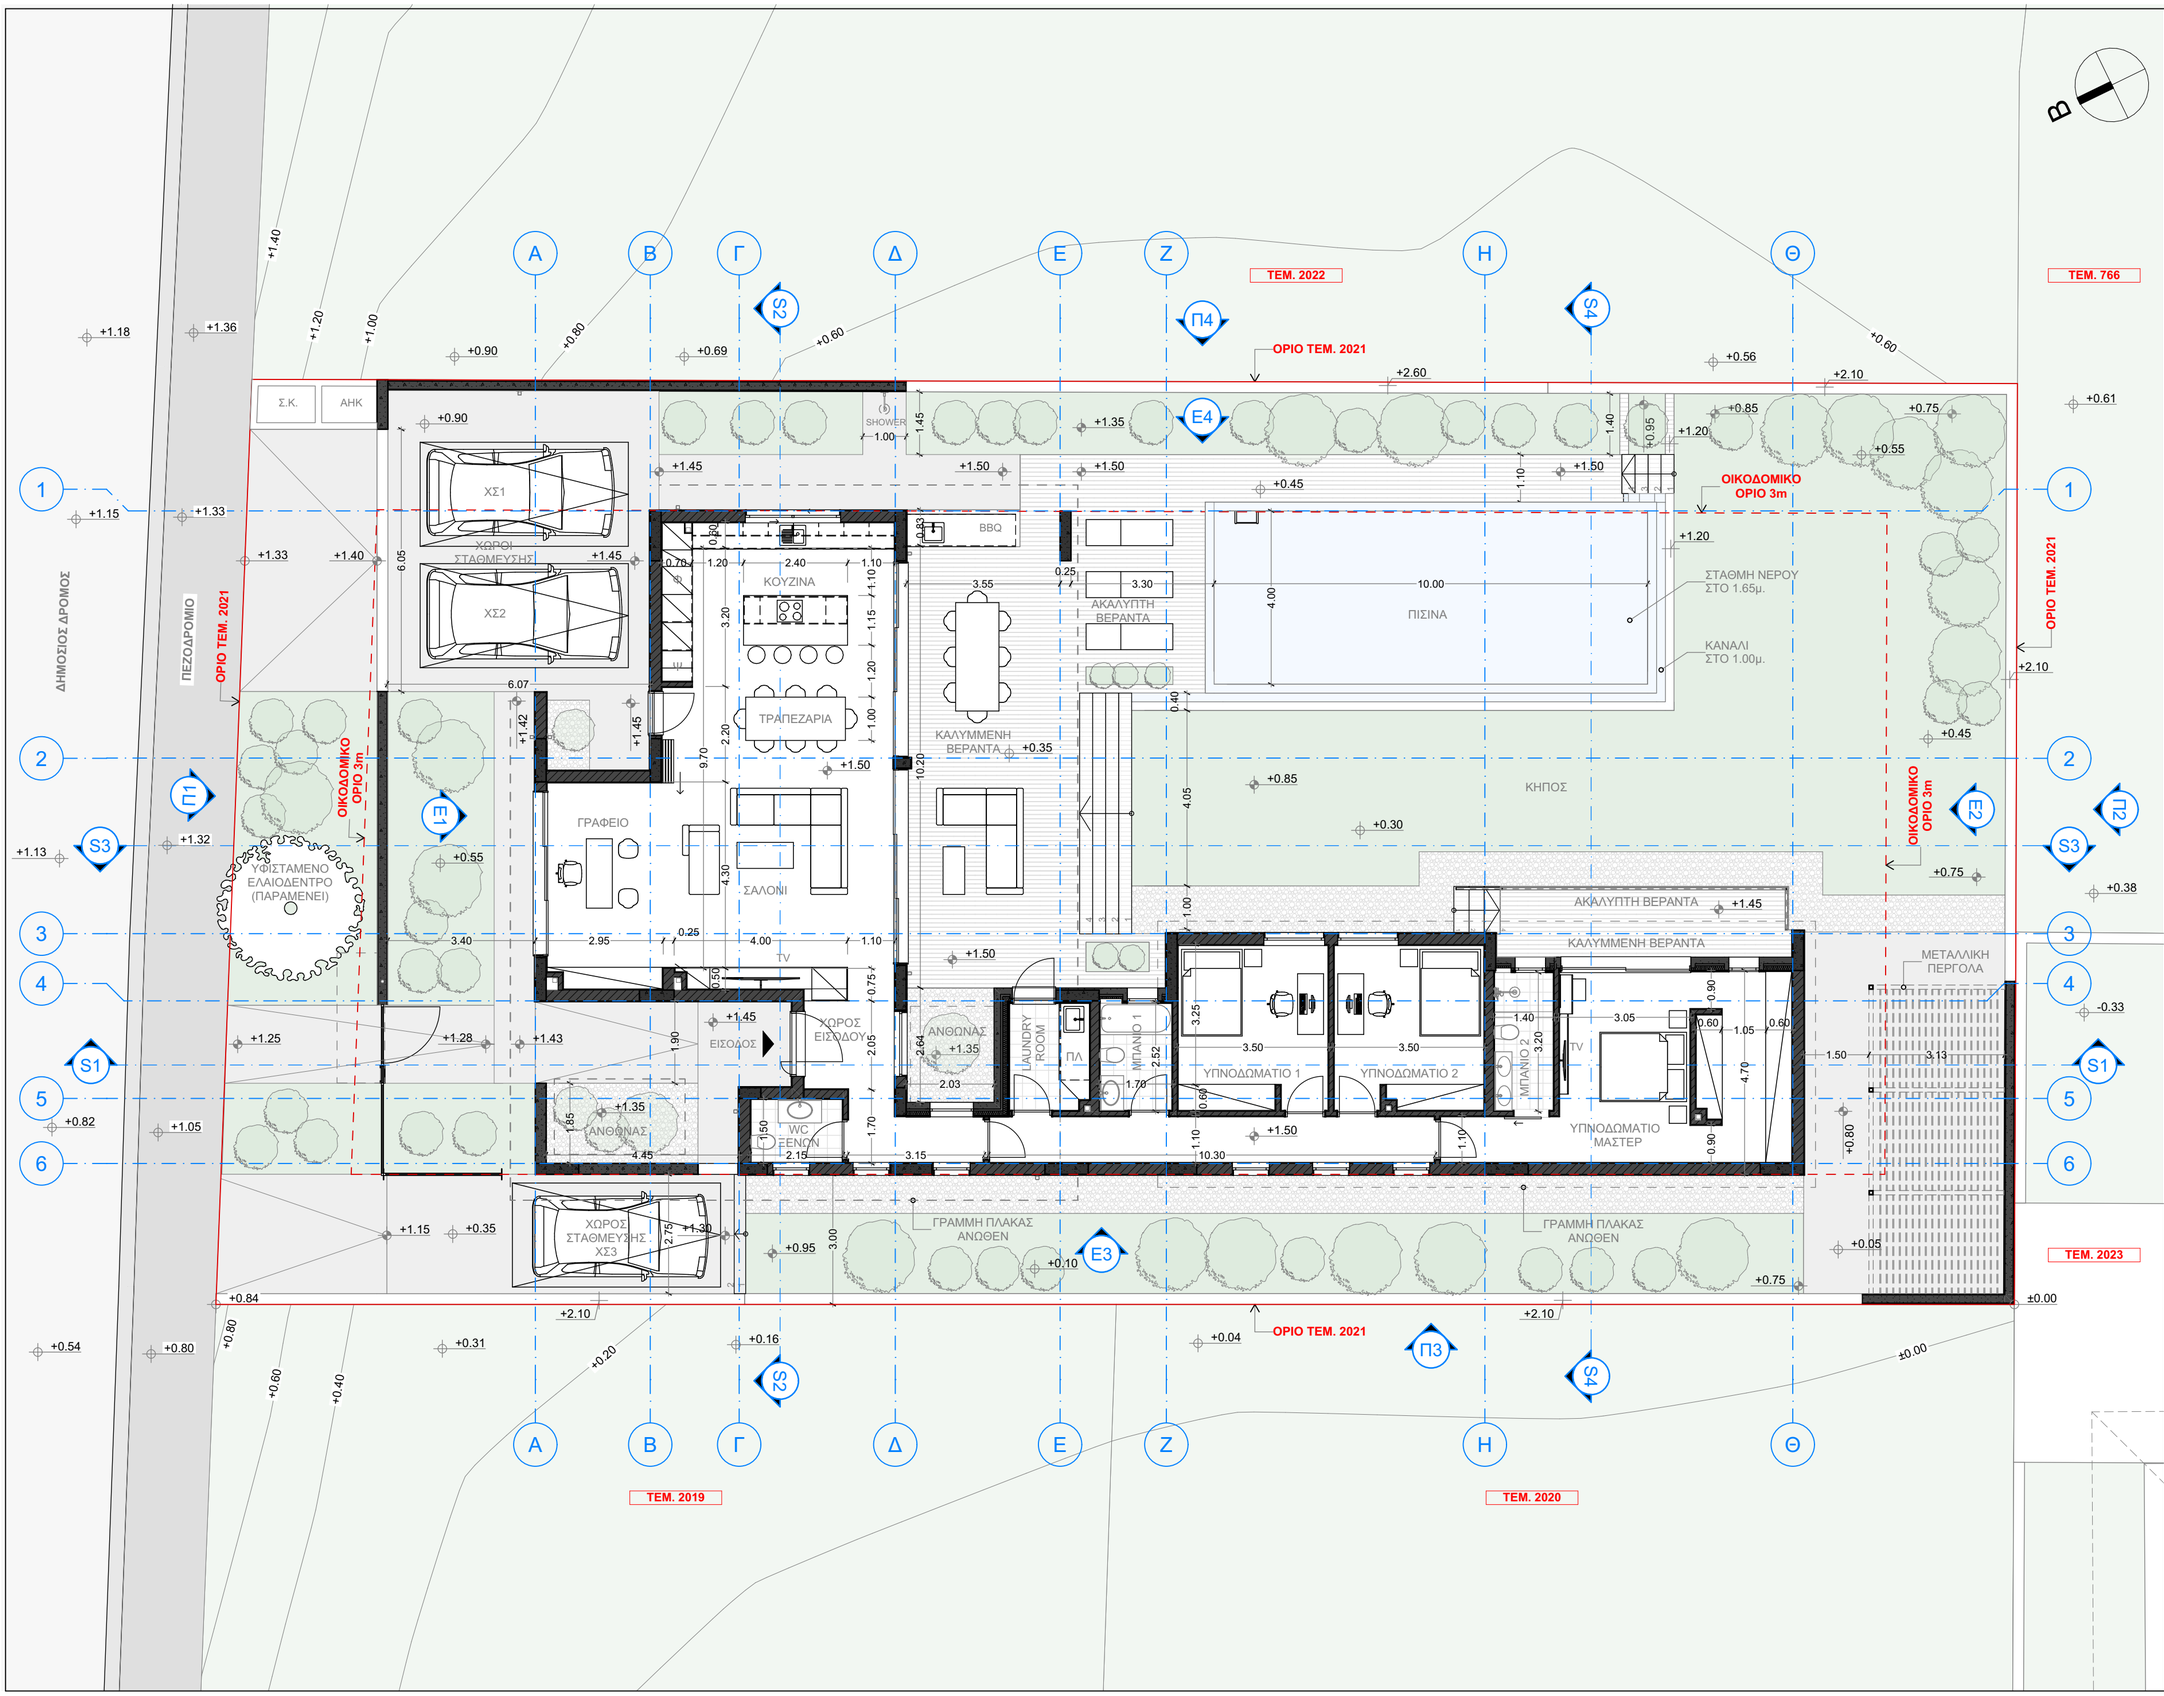

Υπόμνημα Υψομέτρων

— ±000.00 —	ΥΦΙΣΤΑΜΕΝΕΣ ΙΣΟΫΨΕΙΣ ΓΡΑΜΜΕΣ
±000.00	ΥΦΙΣΤΑΜΕΝΑ ΥΨΟΜΕΤΡΑ
±000.00	ΠΡΟΤΕΙΝΟΜΕΝΑ ΥΨΟΜΕΤΡΑ

±0.00μ. = +214μ. (ΠΡΑΓΜΑΤΙΚΟ ΥΨΟΜΕΤΡΟ)

Υπόμνημα Υλικών

1	Μπετόν Σανιδωτό
2	Οπτοπλινθοδομή / Σοβάς
3	Μπετόν / Σοβάς
4	Επένδυση Alucobond
5	Πλέγμα
6	Μεταλλική Πέργολα

Στοιχεία Τεμαχίου

ΤΜΗΜΑ/ΑΡ. ΕΓΓΡΑΦΗΣ: 6/2100
ΦΥΛΛΟ/ΣΧΕΔΙΟ: 30/23Ε2
ΑΡ. ΤΕΜΑΧΙΟΥ: 2021
ΔΗΜΟΣ: ΛΑΤΣΙΩΝ
ΕΝΟΡΙΑ: ΑΓΙΟΣ ΓΕΩΡΓΙΟΣ
ΠΟΛΕΟΔΟΜΙΚΗ ΖΩΝΗ: Κα6

ΕΓΓΕΓΡΑΜΜΕΝΟ ΩΣ ΟΙΚΟΠΕΔΟ

ΣΤΟΙΧΕΙΑ ΕΡΓΟΥ: ΙΣΟΓΕΙΑ ΚΑΤΟΙΚΙΑ
ΔΟΜΗΣΙΜΟ ΕΜΒΑΔΟΝ: 190.00τ.μ.

ΕΝΤΟΛΗ 2/2020
ΠΟΛΕΟΔΟΜΙΚΗ ΑΔΕΙΑ

ΕΥΣΤΑΘΙΟΣ ΛΕΥΚΑΤΗΣ
ΑΡΧΙΤΕΚΤΟΝΑΣ
Α.Μ.ΕΤΕΚ: Α173321

Revision History

RevID	Comment	Date

Αρχιτέκτονας / Architect

LEFKATIS STATHIS ARCHITECTURE

STATHIS LEFKATIS ARCHITECTURE

4, KOURIOU STREET, LATSIA, NICOSIA
CYPRUS, 2220
e-mail: efstathios.lefkatis@gmail.com
tel: 99841485

Κύριος Έργου / Client

ΑΝΤΡΕΑΣ & ΜΑΡΙΑ

Έργο / Project Name

ΙΣΟΓΕΙΑ ΚΑΤΟΙΚΙΑ


Τίτλος Σχεδίου / Drawing Name

ΚΑΤΟΨΗ ΙΣΟΓΕΙΟΥ

Φάση / Design Phase	Μελέτη / Study
ΠΟΛΕΟΔΟΜΙΚΗ ΑΔΕΙΑ	**ΑΡΧΙΤΕΚΤΟΝΙΚΗ**
Checked by	Ημερομηνία / Date
ΣΤΑΘΗΣ ΛΕΥΚΑΤΗΣ	**19/03/2026**
Layout ID	Revision
A1.2	

Κλίμακα Σχεδίου / Drawing Scale

1:100 @ A2

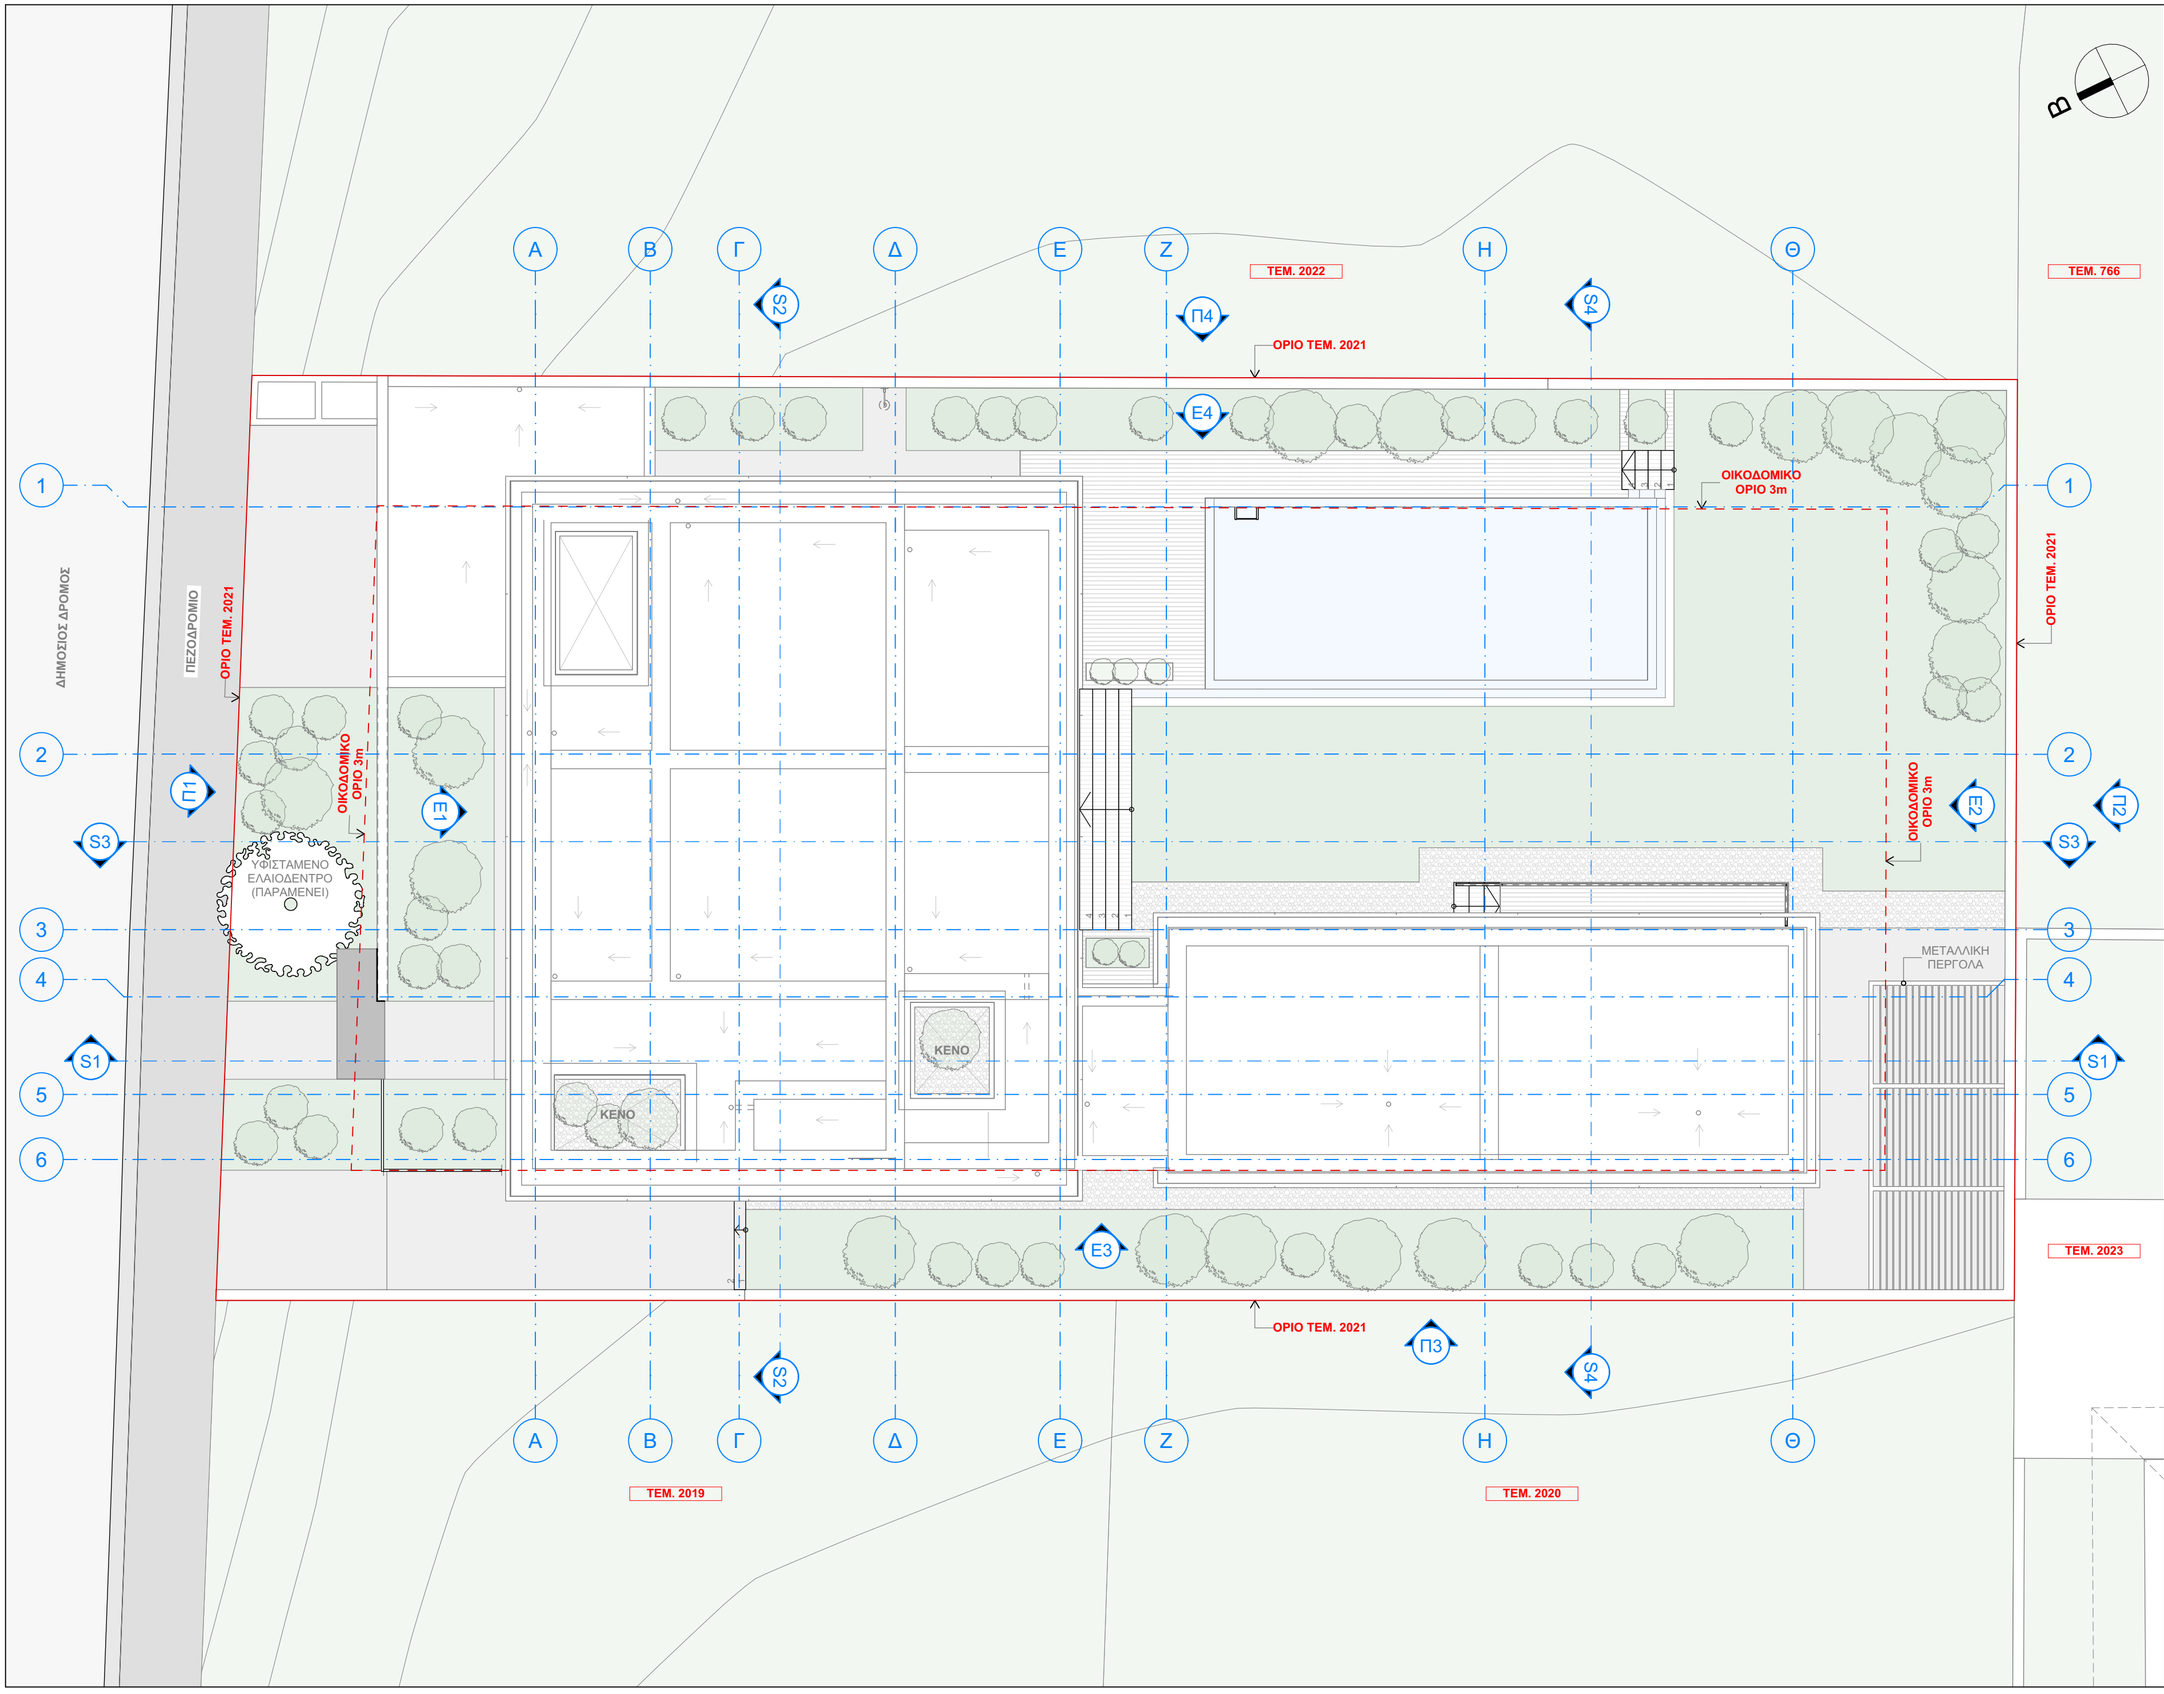

Υπόμνημα Υψομέτρων

— ±000.00 —	ΥΦΙΣΤΑΜΕΝΕΣ ΙΣΟΫΨΕΙΣ ΓΡΑΜΜΕΣ
±000.00	ΥΦΙΣΤΑΜΕΝΑ ΥΨΟΜΕΤΡΑ
±000.00	ΠΡΟΤΕΙΝΟΜΕΝΑ ΥΨΟΜΕΤΡΑ

±0.00μ. = +214μ. (ΠΡΑΓΜΑΤΙΚΟ ΥΨΟΜΕΤΡΟ)

Υπόμνημα Υλικών

1	Μπετόν Σανιδωτό
2	Οπτοπλινθοδομή / Σοβάς
3	Μπετόν / Σοβάς
4	Επένδυση Alucobond
5	Πλέγμα
6	Μεταλλική Πέργολα

Στοιχεία Τεμαχίου

ΤΜΗΜΑ/ΑΡ. ΕΓΓΡΑΦΗΣ: 6/2100
ΦΥΛΛΟ/ΣΧΕΔΙΟ: 30/23Ε2
ΑΡ. ΤΕΜΑΧΙΟΥ: 2021
ΔΗΜΟΣ: ΛΑΤΣΙΩΝ
ΕΝΟΡΙΑ: ΑΓΙΟΣ ΓΕΩΡΓΙΟΣ
ΠΟΛΕΟΔΟΜΙΚΗ ΖΩΝΗ: Κα6

ΕΓΓΕΓΡΑΜΜΕΝΟ ΩΣ ΟΙΚΟΠΕΔΟ

ΣΤΟΙΧΕΙΑ ΕΡΓΟΥ: ΙΣΟΓΕΙΑ ΚΑΤΟΙΚΙΑ
ΔΟΜΗΣΙΜΟ ΕΜΒΑΔΟΝ: 190.00τ.μ.

ΕΝΤΟΛΗ 2/2020
ΠΟΛΕΟΔΟΜΙΚΗ ΑΔΕΙΑ

ΕΥΣΤΑΘΙΟΣ ΛΕΥΚΑΤΗΣ
ΑΡΧΙΤΕΚΤΟΝΑΣ
Α.Μ.ΕΤΕΚ: Α173321

Revision History

RevID	Comment	Date

Αρχιτέκτονας / Architect

LEFKATIS STATHIS ARCHITECTURE

STATHIS LEFKATIS ARCHITECTURE

4, KOURIOU STREET, LATSIA, NICOSIA
CYPRUS, 2220
e-mail: efstathios.lefkatis@gmail.com
tel: 99841485

Κύριος Έργου / Client

ΑΝΤΡΕΑΣ & ΜΑΡΙΑ

Έργο / Project Name

ΙΣΟΓΕΙΑ ΚΑΤΟΙΚΙΑ


Τίτλος Σχεδίου / Drawing Name


ΚΑΤΟΨΗ ΟΡΟΦΗΣ

Φάση / Design Phase	Μελέτη / Study
ΠΟΛΕΟΔΟΜΙΚΗ ΑΔΕΙΑ	**ΑΡΧΙΤΕΚΤΟΝΙΚΗ**
Checked by	Ημερομηνία / Date
ΣΤΑΘΗΣ ΛΕΥΚΑΤΗΣ	**19/03/2026**
Layout ID	Revision
A1.3	

Κλίμακα Σχεδίου / Drawing Scale

1:100 @ A2

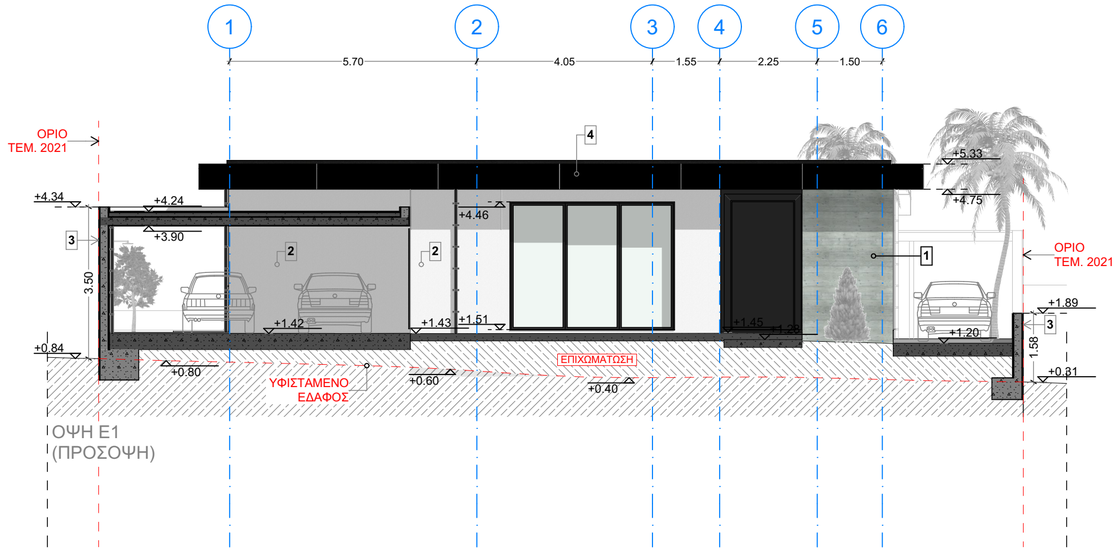

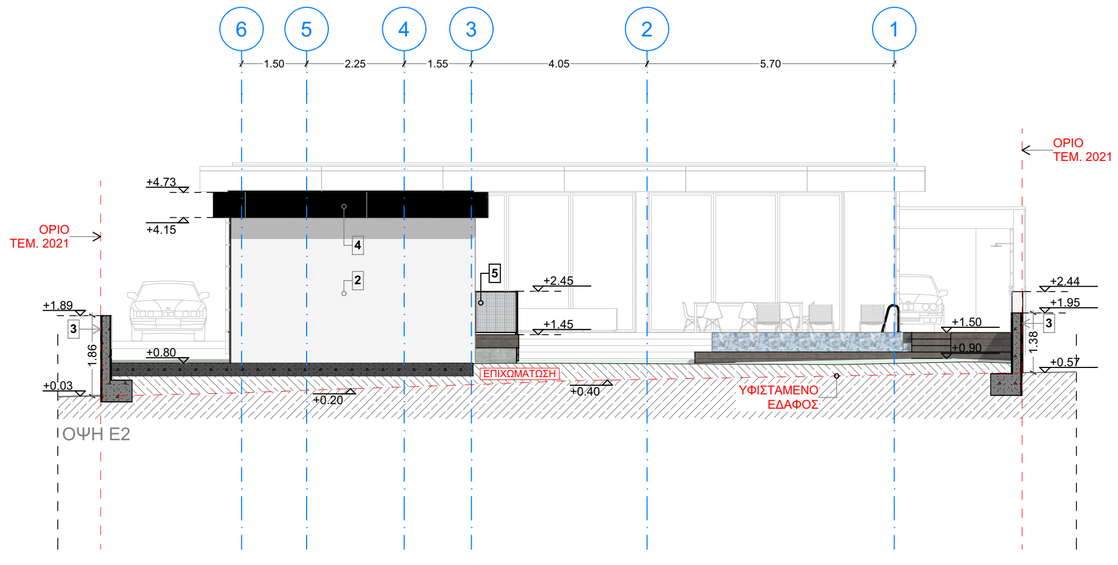

Υπόμνημα Υψομέτρων

— ±000.00 —	ΥΦΙΣΤΑΜΕΝΕΣ ΙΣΟΫΨΕΙΣ ΓΡΑΜΜΕΣ
±000.00	ΥΦΙΣΤΑΜΕΝΑ ΥΨΟΜΕΤΡΑ
±000.00	ΠΡΟΤΕΙΝΟΜΕΝΑ ΥΨΟΜΕΤΡΑ

±0.00μ. = +214μ. (ΠΡΑΓΜΑΤΙΚΟ ΥΨΟΜΕΤΡΟ)

Υπόμνημα Υλικών

1	Μπετόν Σανιδωτό
2	Οπτοπλινθοδομή / Σοβάς
3	Μπετόν / Σοβάς
4	Επένδυση Alucobond
5	Πλέγμα
6	Μεταλλική Πέργολα

Στοιχεία Τεμαχίου

ΤΜΗΜΑ/ΑΡ. ΕΓΓΡΑΦΗΣ: 6/2100
ΦΥΛΛΟ/ΣΧΕΔΙΟ: 30/23Ε2
ΑΡ. ΤΕΜΑΧΙΟΥ: 2021
ΔΗΜΟΣ: ΛΑΤΣΙΩΝ
ΕΝΟΡΙΑ: ΑΓΙΟΣ ΓΕΩΡΓΙΟΣ
ΠΟΛΕΟΔΟΜΙΚΗ ΖΩΝΗ: Κα6

ΕΓΓΕΓΡΑΜΜΕΝΟ ΩΣ ΟΙΚΟΠΕΔΟ

ΣΤΟΙΧΕΙΑ ΕΡΓΟΥ: ΙΣΟΓΕΙΑ ΚΑΤΟΙΚΙΑ
ΔΟΜΗΣΙΜΟ ΕΜΒΑΔΟΝ: 190.00τ.μ.

ΕΝΤΟΛΗ 2/2020
ΠΟΛΕΟΔΟΜΙΚΗ ΑΔΕΙΑ

ΕΥΣΤΑΘΙΟΣ ΛΕΥΚΑΤΗΣ
ΑΡΧΙΤΕΚΤΟΝΑΣ
Α.Μ.ΕΤΕΚ: Α173321

Revision History

RevID	Comment	Date

Αρχιτέκτονας / Architect

LEFKATIS STATHIS ARCHITECTURE

STATHIS LEFKATIS ARCHITECTURE

4, KOURIOU STREET, LATSIA, NICOSIA
CYPRUS, 2220
e-mail: efstathios.lefkatis@gmail.com
tel: 99841485

Κύριος Έργου / Client

ΑΝΤΡΕΑΣ & ΜΑΡΙΑ

Έργο / Project Name

ΙΣΟΓΕΙΑ ΚΑΤΟΙΚΙΑ


Τίτλος Σχεδίου / Drawing Name


ΟΨΕΙΣ

Φάση / Design Phase	Μελέτη / Study
ΠΟΛΕΟΔΟΜΙΚΗ ΑΔΕΙΑ	**ΑΡΧΙΤΕΚΤΟΝΙΚΗ**
Checked by	Ημερομηνία / Date
ΣΤΑΘΗΣ ΛΕΥΚΑΤΗΣ	**19/03/2026**
Layout ID	Revision
A2.1	

Κλίμακα Σχεδίου / Drawing Scale

1:100 @ A2

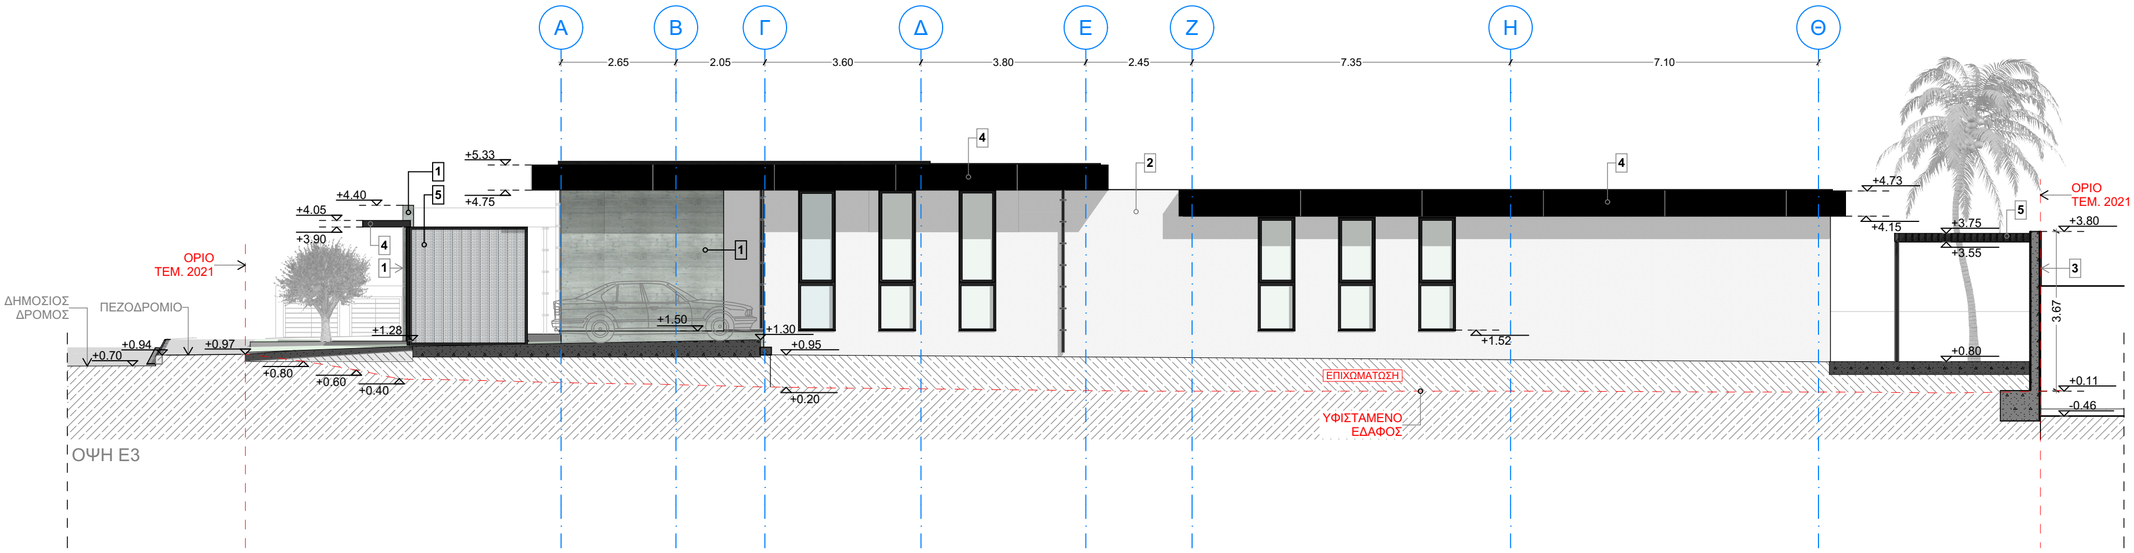

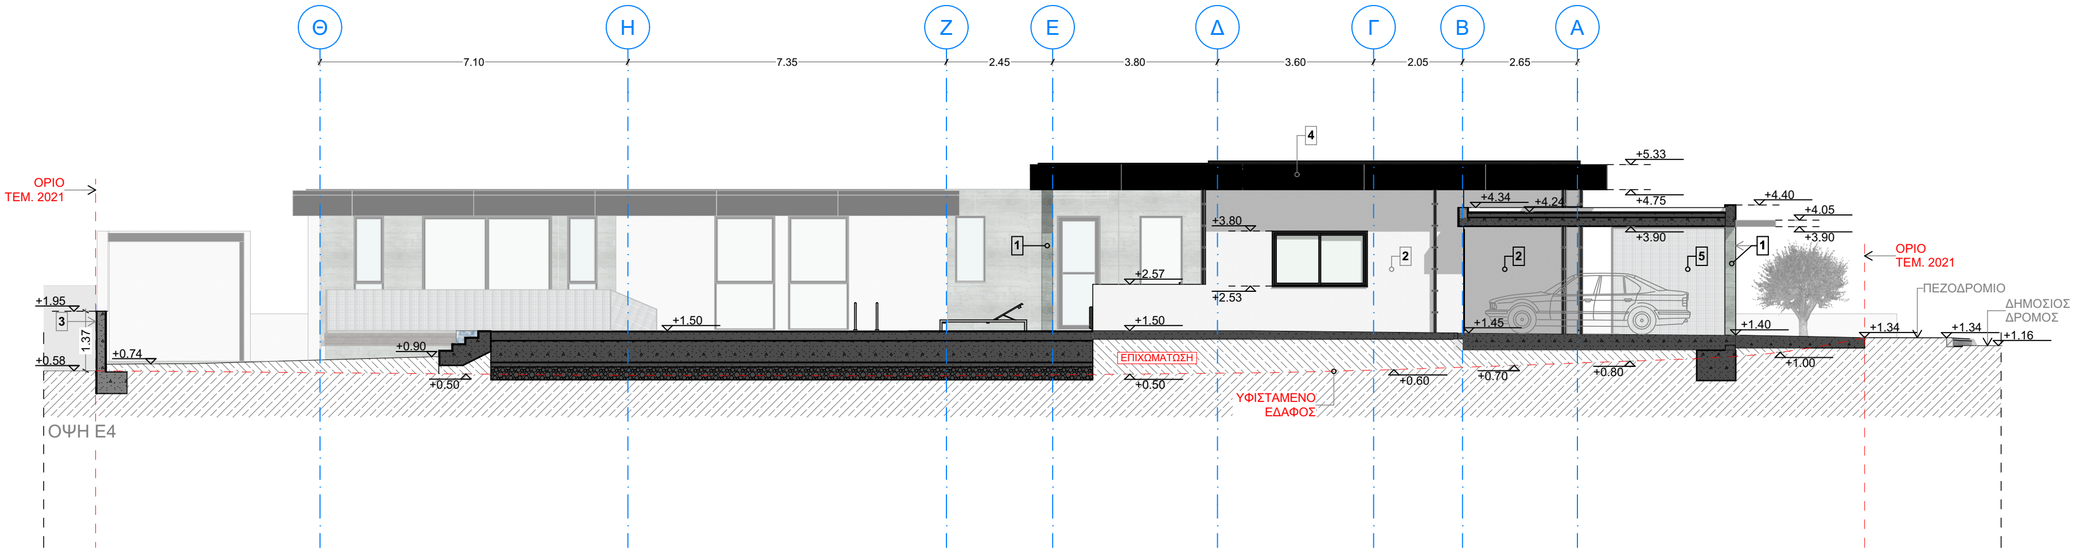

Υπόμνημα Υψομέτρων

— ±000.00 —	ΥΦΙΣΤΑΜΕΝΕΣ ΙΣΟΫΨΕΙΣ ΓΡΑΜΜΕΣ
±000.00	ΥΦΙΣΤΑΜΕΝΑ ΥΨΟΜΕΤΡΑ
±000.00	ΠΡΟΤΕΙΝΟΜΕΝΑ ΥΨΟΜΕΤΡΑ

±0.00μ. = +214μ. (ΠΡΑΓΜΑΤΙΚΟ ΥΨΟΜΕΤΡΟ)

Υπόμνημα Υλικών

1	Μπετόν Σανιδωτό
2	Οπτοπλινθοδομή / Σοβάς
3	Μπετόν / Σοβάς
4	Επένδυση Alucobond
5	Πλέγμα
6	Μεταλλική Πέργολα

Στοιχεία Τεμαχίου

ΤΜΗΜΑ/ΑΡ. ΕΓΓΡΑΦΗΣ: 6/2100
ΦΥΛΛΟ/ΣΧΕΔΙΟ: 30/23Ε2
ΑΡ. ΤΕΜΑΧΙΟΥ: 2021
ΔΗΜΟΣ: ΛΑΤΣΙΩΝ
ΕΝΟΡΙΑ: ΑΓΙΟΣ ΓΕΩΡΓΙΟΣ
ΠΟΛΕΟΔΟΜΙΚΗ ΖΩΝΗ: Κα6

ΕΓΓΕΓΡΑΜΜΕΝΟ ΩΣ ΟΙΚΟΠΕΔΟ

ΣΤΟΙΧΕΙΑ ΕΡΓΟΥ: ΙΣΟΓΕΙΑ ΚΑΤΟΙΚΙΑ
ΔΟΜΗΣΙΜΟ ΕΜΒΑΔΟΝ: 190.00τ.μ.

ΕΝΤΟΛΗ 2/2020
ΠΟΛΕΟΔΟΜΙΚΗ ΑΔΕΙΑ

ΕΥΣΤΑΘΙΟΣ ΛΕΥΚΑΤΗΣ
ΑΡΧΙΤΕΚΤΟΝΑΣ
Α.Μ.ΕΤΕΚ: Α173321

Revision History

RevID	Comment	Date

Αρχιτέκτονας / Architect

LEFKATIS STATHIS ARCHITECTURE

STATHIS LEFKATIS ARCHITECTURE

4, KOURIOU STREET, LATSIA, NICOSIA
CYPRUS, 2220
e-mail: efstathios.lefkatis@gmail.com
tel: 99841485

Κύριος Έργου / Client

ΑΝΤΡΕΑΣ & ΜΑΡΙΑ

Έργο / Project Name

ΙΣΟΓΕΙΑ ΚΑΤΟΙΚΙΑ


Τίτλος Σχεδίου / Drawing Name


ΟΨΕΙΣ

Φάση / Design Phase	Μελέτη / Study
ΠΟΛΕΟΔΟΜΙΚΗ ΑΔΕΙΑ	**ΑΡΧΙΤΕΚΤΟΝΙΚΗ**
Checked by	Ημερομηνία / Date
ΣΤΑΘΗΣ ΛΕΥΚΑΤΗΣ	**19/03/2026**
Layout ID	Revision
A2.2	

Κλίμακα Σχεδίου / Drawing Scale

1:100 @ A2

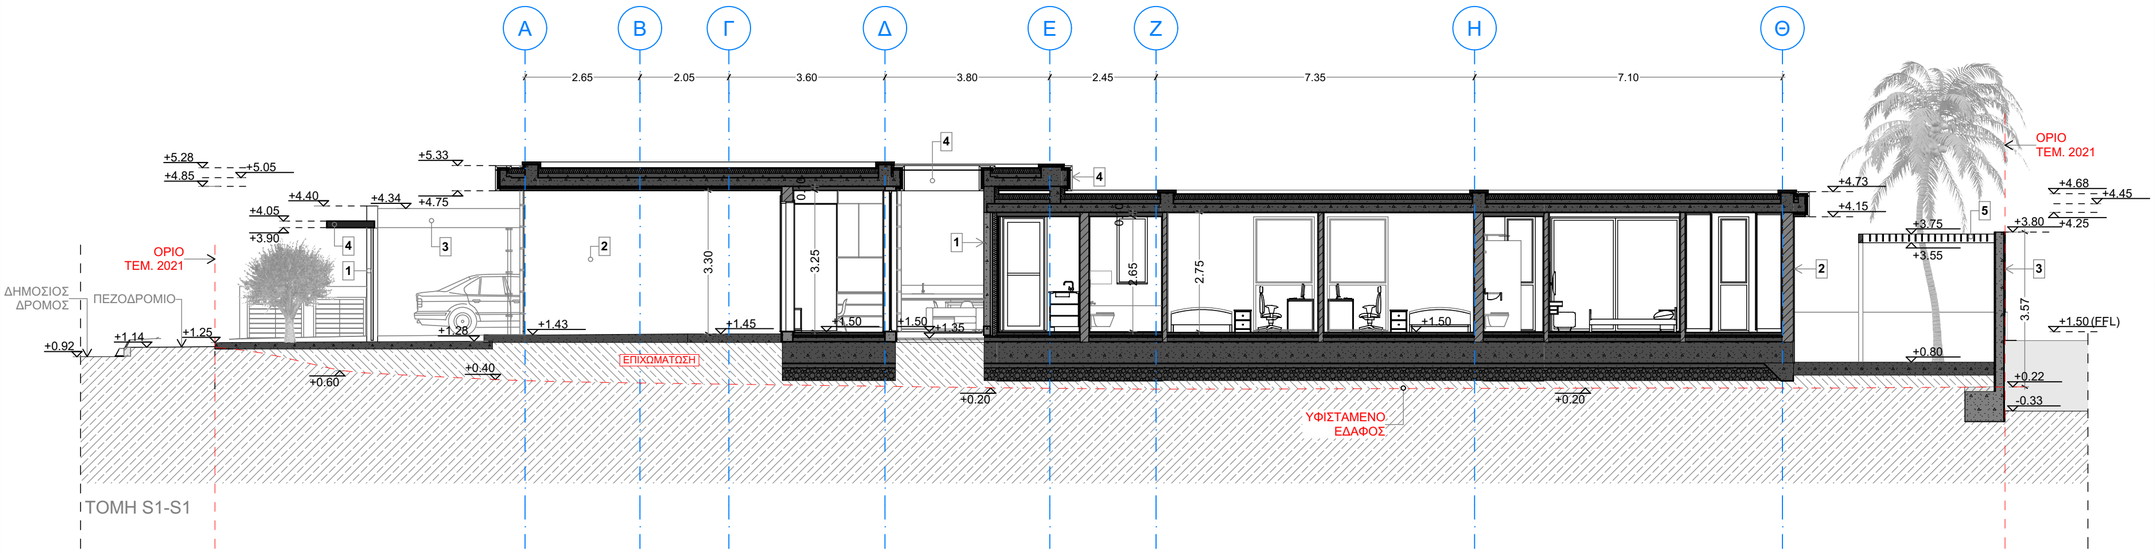

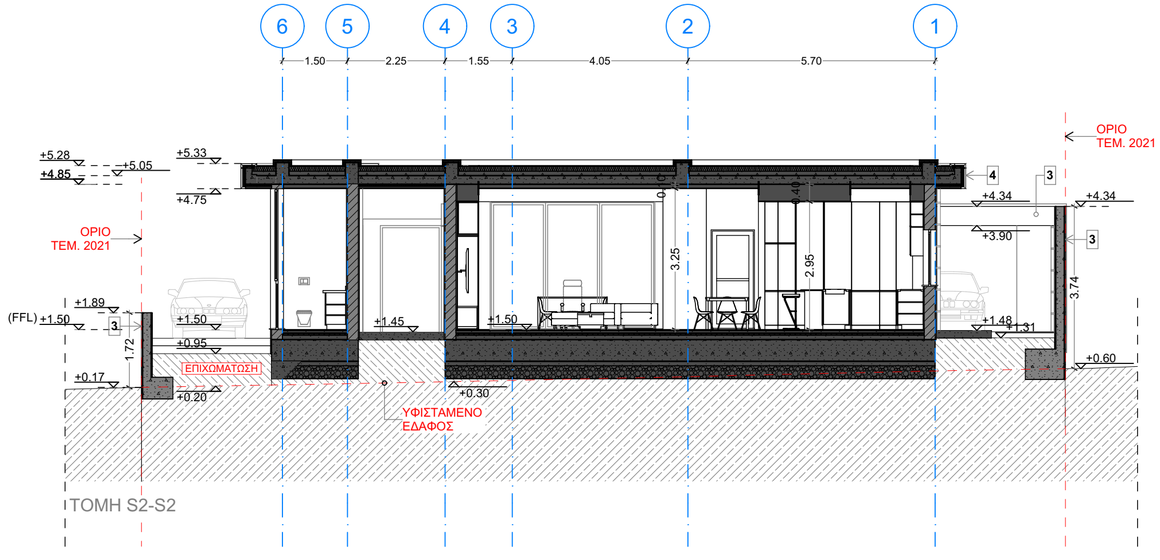

Υπόμνημα Υψομέτρων

— ±000.00 —	ΥΦΙΣΤΑΜΕΝΕΣ ΙΣΟΫΨΕΙΣ ΓΡΑΜΜΕΣ
±000.00	ΥΦΙΣΤΑΜΕΝΑ ΥΨΟΜΕΤΡΑ
±000.00	ΠΡΟΤΕΙΝΟΜΕΝΑ ΥΨΟΜΕΤΡΑ

±0.00μ. = +214μ. (ΠΡΑΓΜΑΤΙΚΟ ΥΨΟΜΕΤΡΟ)

Υπόμνημα Υλικών

1	Μπετόν Σανιδωτό
2	Οπτοπλινθοδομή / Σοβάς
3	Μπετόν / Σοβάς
4	Επένδυση Alucobond
5	Πλέγμα
6	Μεταλλική Πέργολα

Στοιχεία Τεμαχίου

ΤΜΗΜΑ/ΑΡ. ΕΓΓΡΑΦΗΣ: 6/2100
ΦΥΛΛΟ/ΣΧΕΔΙΟ: 30/23Ε2
ΑΡ. ΤΕΜΑΧΙΟΥ: 2021
ΔΗΜΟΣ: ΛΑΤΣΙΩΝ
ΕΝΟΡΙΑ: ΑΓΙΟΣ ΓΕΩΡΓΙΟΣ
ΠΟΛΕΟΔΟΜΙΚΗ ΖΩΝΗ: Κα6

ΕΓΓΕΓΡΑΜΜΕΝΟ ΩΣ ΟΙΚΟΠΕΔΟ

ΣΤΟΙΧΕΙΑ ΕΡΓΟΥ: ΙΣΟΓΕΙΑ ΚΑΤΟΙΚΙΑ
ΔΟΜΗΣΙΜΟ ΕΜΒΑΔΟΝ: 190.00τ.μ.

ΕΝΤΟΛΗ 2/2020
ΠΟΛΕΟΔΟΜΙΚΗ ΑΔΕΙΑ

ΕΥΣΤΑΘΙΟΣ ΛΕΥΚΑΤΗΣ
ΑΡΧΙΤΕΚΤΟΝΑΣ
Α.Μ.ΕΤΕΚ: Α173321

Revision History

RevID	Comment	Date

Αρχιτέκτονας / Architect

LEFKATIS STATHIS ARCHITECTURE

STATHIS LEFKATIS ARCHITECTURE

4, KOURIOU STREET, LATSIA, NICOSIA
CYPRUS, 2220
e-mail: efstathios.lefkatis@gmail.com
tel: 99841485

Κύριος Έργου / Client

ΑΝΤΡΕΑΣ & ΜΑΡΙΑ

Έργο / Project Name

ΙΣΟΓΕΙΑ ΚΑΤΟΙΚΙΑ


Τίτλος Σχεδίου / Drawing Name


ΤΟΜΕΣ

Φάση / Design Phase	Μελέτη / Study
ΠΟΛΕΟΔΟΜΙΚΗ ΑΔΕΙΑ	**ΑΡΧΙΤΕΚΤΟΝΙΚΗ**
Checked by	Ημερομηνία / Date
ΣΤΑΘΗΣ ΛΕΥΚΑΤΗΣ	**20/03/2026**
Layout ID	Revision
A3.1	

Κλίμακα Σχεδίου / Drawing Scale

1:100 @ A2

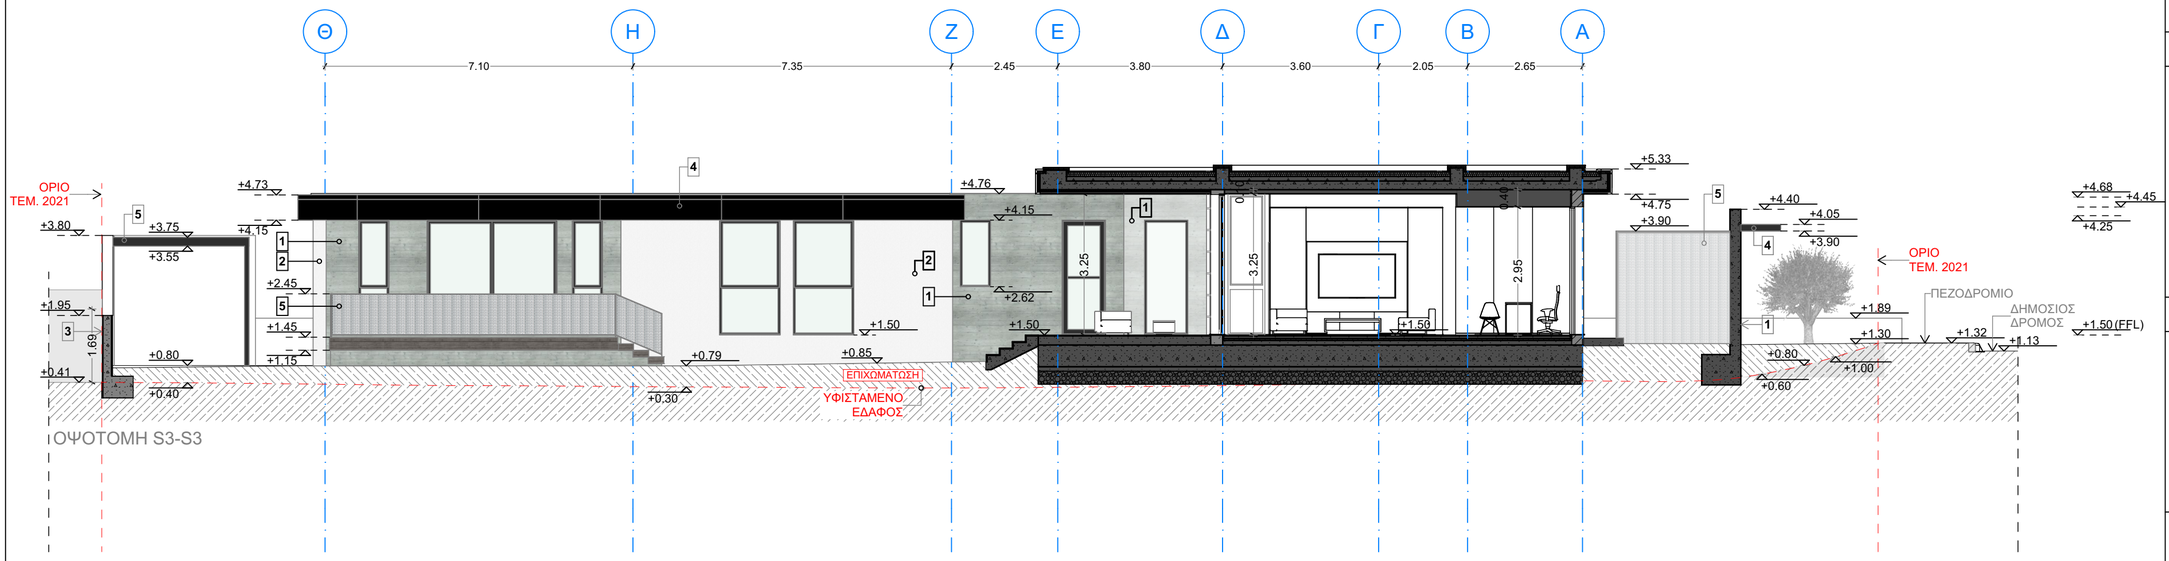

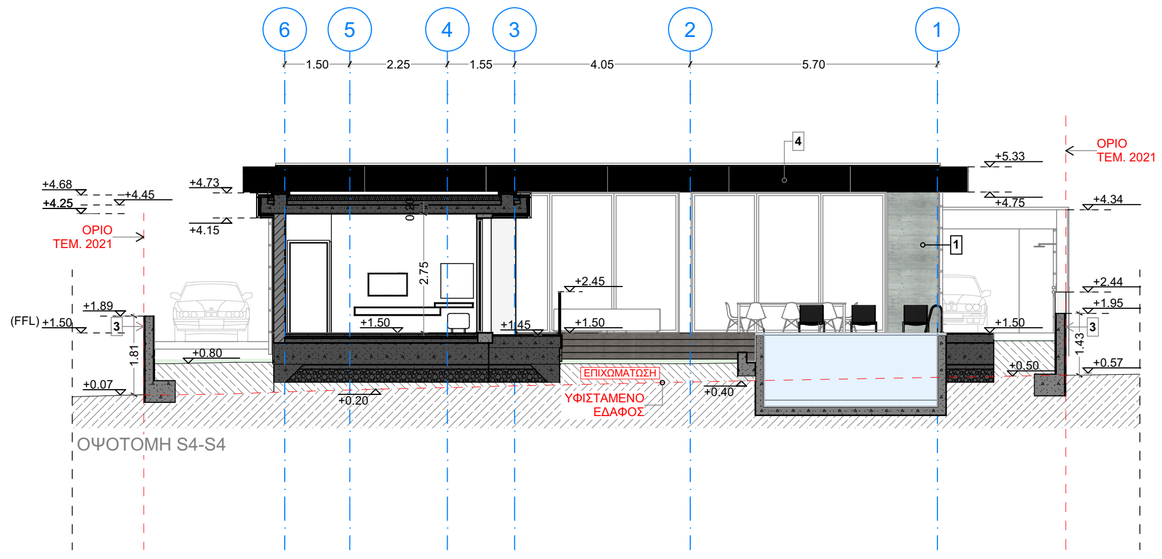

Υπόμνημα Υψομέτρων

— ±000.00 —	ΥΦΙΣΤΑΜΕΝΕΣ ΙΣΟΫΨΕΙΣ ΓΡΑΜΜΕΣ
±000.00	ΥΦΙΣΤΑΜΕΝΑ ΥΨΟΜΕΤΡΑ
±000.00	ΠΡΟΤΕΙΝΟΜΕΝΑ ΥΨΟΜΕΤΡΑ

±0.00μ. = +214μ. (ΠΡΑΓΜΑΤΙΚΟ ΥΨΟΜΕΤΡΟ)

Υπόμνημα Υλικών

1	Μπετόν Σανιδωτό
2	Οπτοπλινθοδομή / Σοβάς
3	Μπετόν / Σοβάς
4	Επένδυση Alucobond
5	Πλέγμα
6	Μεταλλική Πέργολα

Στοιχεία Τεμαχίου

ΤΜΗΜΑ/ΑΡ. ΕΓΓΡΑΦΗΣ: 6/2100
ΦΥΛΛΟ/ΣΧΕΔΙΟ: 30/23Ε2
ΑΡ. ΤΕΜΑΧΙΟΥ: 2021
ΔΗΜΟΣ: ΛΑΤΣΙΩΝ
ΕΝΟΡΙΑ: ΑΓΙΟΣ ΓΕΩΡΓΙΟΣ
ΠΟΛΕΟΔΟΜΙΚΗ ΖΩΝΗ: Κα6

ΕΓΓΕΓΡΑΜΜΕΝΟ ΩΣ ΟΙΚΟΠΕΔΟ

ΣΤΟΙΧΕΙΑ ΕΡΓΟΥ: ΙΣΟΓΕΙΑ ΚΑΤΟΙΚΙΑ
ΔΟΜΗΣΙΜΟ ΕΜΒΑΔΟΝ: 190.00τ.μ.

ΕΝΤΟΛΗ 2/2020
ΠΟΛΕΟΔΟΜΙΚΗ ΑΔΕΙΑ

ΕΥΣΤΑΘΙΟΣ ΛΕΥΚΑΤΗΣ
ΑΡΧΙΤΕΚΤΟΝΑΣ
Α.Μ.ΕΤΕΚ: Α173321

Revision History

RevID	Comment	Date

Αρχιτέκτονας / Architect

LEFKATIS STATHIS ARCHITECTURE

STATHIS LEFKATIS ARCHITECTURE

4, KOURIOU STREET, LATSIA, NICOSIA
CYPRUS, 2220
e-mail: efstathios.lefkatis@gmail.com
tel: 99841485

Κύριος Έργου / Client

ΑΝΤΡΕΑΣ & ΜΑΡΙΑ

Έργο / Project Name

ΙΣΟΓΕΙΑ ΚΑΤΟΙΚΙΑ


Τίτλος Σχεδίου / Drawing Name


ΟΨΟΤΟΜΕΣ


Φάση / Design Phase	Μελέτη / Study
ΠΟΛΕΟΔΟΜΙΚΗ ΑΔΕΙΑ	**ΑΡΧΙΤΕΚΤΟΝΙΚΗ**
Checked by	Ημερομηνία / Date
ΣΤΑΘΗΣ ΛΕΥΚΑΤΗΣ	**20/03/2026**
Layout ID	Revision
A3.2	


Κλίμακα Σχεδίου / Drawing Scale


1:100 @ A2

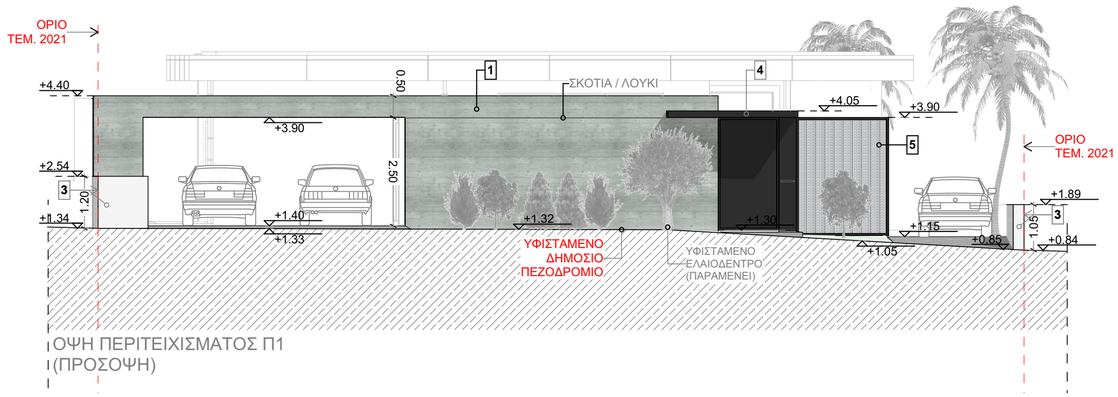

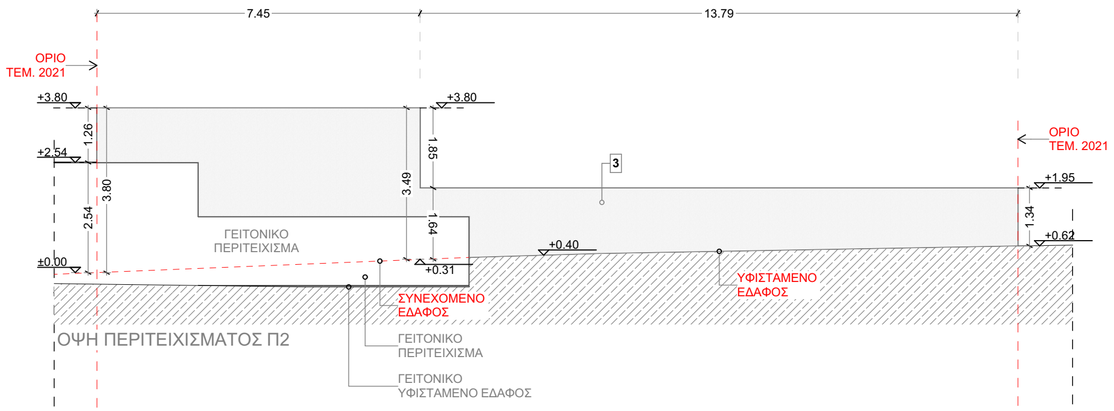

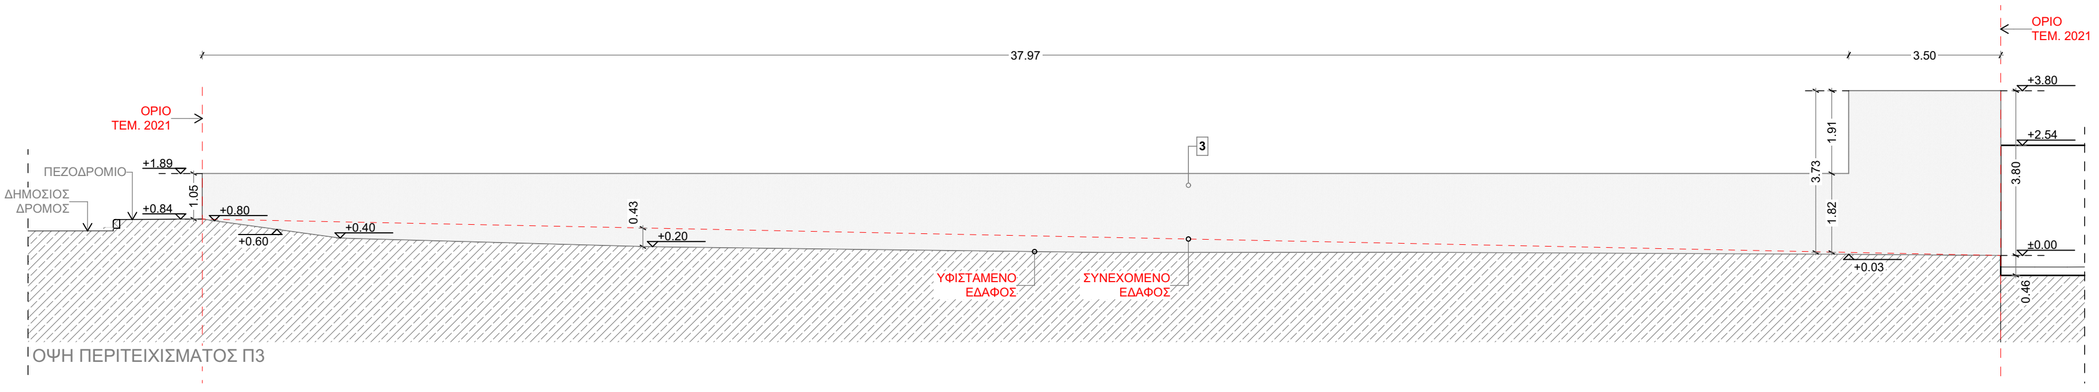

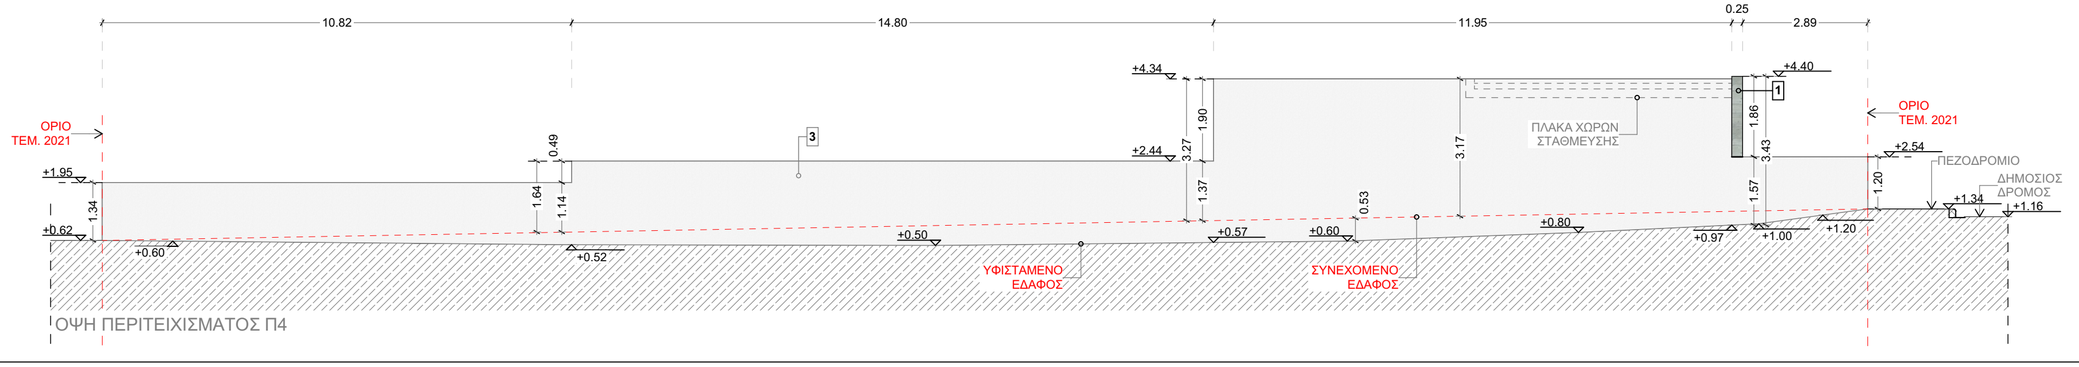

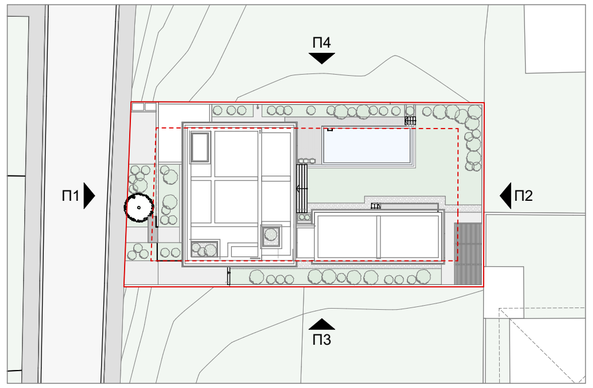

ΚΑΤΟΨΗ 1:500

Υπόμνημα Υψομέτρων

— ±000.00 —	ΥΦΙΣΤΑΜΕΝΕΣ ΙΣΟΫΨΕΙΣ ΓΡΑΜΜΕΣ
±000.00	ΥΦΙΣΤΑΜΕΝΑ ΥΨΟΜΕΤΡΑ
±000.00	ΠΡΟΤΕΙΝΟΜΕΝΑ ΥΨΟΜΕΤΡΑ

±0.00μ. = +214μ. (ΠΡΑΓΜΑΤΙΚΟ ΥΨΟΜΕΤΡΟ)

Υπόμνημα Υλικών

1	Μπετόν Σανιδωτό
2	Οπτοπλινθοδομή / Σοβάς
3	Μπετόν / Σοβάς
4	Επένδυση Alucobond
5	Πλέγμα
6	Μεταλλική Πέργολα

Στοιχεία Τεμαχίου

ΤΜΗΜΑ/ΑΡ. ΕΓΓΡΑΦΗΣ: 6/2100
ΦΥΛΛΟ/ΣΧΕΔΙΟ: 30/23Ε2
ΑΡ. ΤΕΜΑΧΙΟΥ: 2021
ΔΗΜΟΣ: ΛΑΤΣΙΩΝ
ΕΝΟΡΙΑ: ΑΓΙΟΣ ΓΕΩΡΓΙΟΣ
ΠΟΛΕΟΔΟΜΙΚΗ ΖΩΝΗ: Κα6

ΕΓΓΕΓΡΑΜΜΕΝΟ ΩΣ ΟΙΚΟΠΕΔΟ

ΣΤΟΙΧΕΙΑ ΕΡΓΟΥ: ΙΣΟΓΕΙΑ ΚΑΤΟΙΚΙΑ
ΔΟΜΗΣΙΜΟ ΕΜΒΑΔΟΝ: 190.00τ.μ.

ΕΝΤΟΛΗ 2/2020
ΠΟΛΕΟΔΟΜΙΚΗ ΑΔΕΙΑ

ΕΥΣΤΑΘΙΟΣ ΛΕΥΚΑΤΗΣ
ΑΡΧΙΤΕΚΤΟΝΑΣ
Α.Μ.ΕΤΕΚ: Α173321

Revision History

RevID	Comment	Date

Αρχιτέκτονας / Architect

LEFKATIS STATHIS ARCHITECTURE

STATHIS LEFKATIS ARCHITECTURE

4, KOURIOU STREET, LATSIA, NICOSIA
CYPRUS, 2220
e-mail: efstathios.lefkatis@gmail.com
tel: 99841485

Κύριος Έργου / Client

ΑΝΤΡΕΑΣ & ΜΑΡΙΑ

Έργο / Project Name

ΙΣΟΓΕΙΑ ΚΑΤΟΙΚΙΑ


Τίτλος Σχεδίου / Drawing Name

ΠΕΡΙΤΕΙΧΙΣΜΑΤΑ

Φάση / Design Phase	Μελέτη / Study
ΠΟΛΕΟΔΟΜΙΚΗ ΑΔΕΙΑ	**ΑΡΧΙΤΕΚΤΟΝΙΚΗ**
Checked by	Ημερομηνία / Date
ΣΤΑΘΗΣ ΛΕΥΚΑΤΗΣ	**20/03/2026**
Layout ID	Revision
A4	

Κλίμακα Σχεδίου / Drawing Scale

1:100, 1:500 @ A2

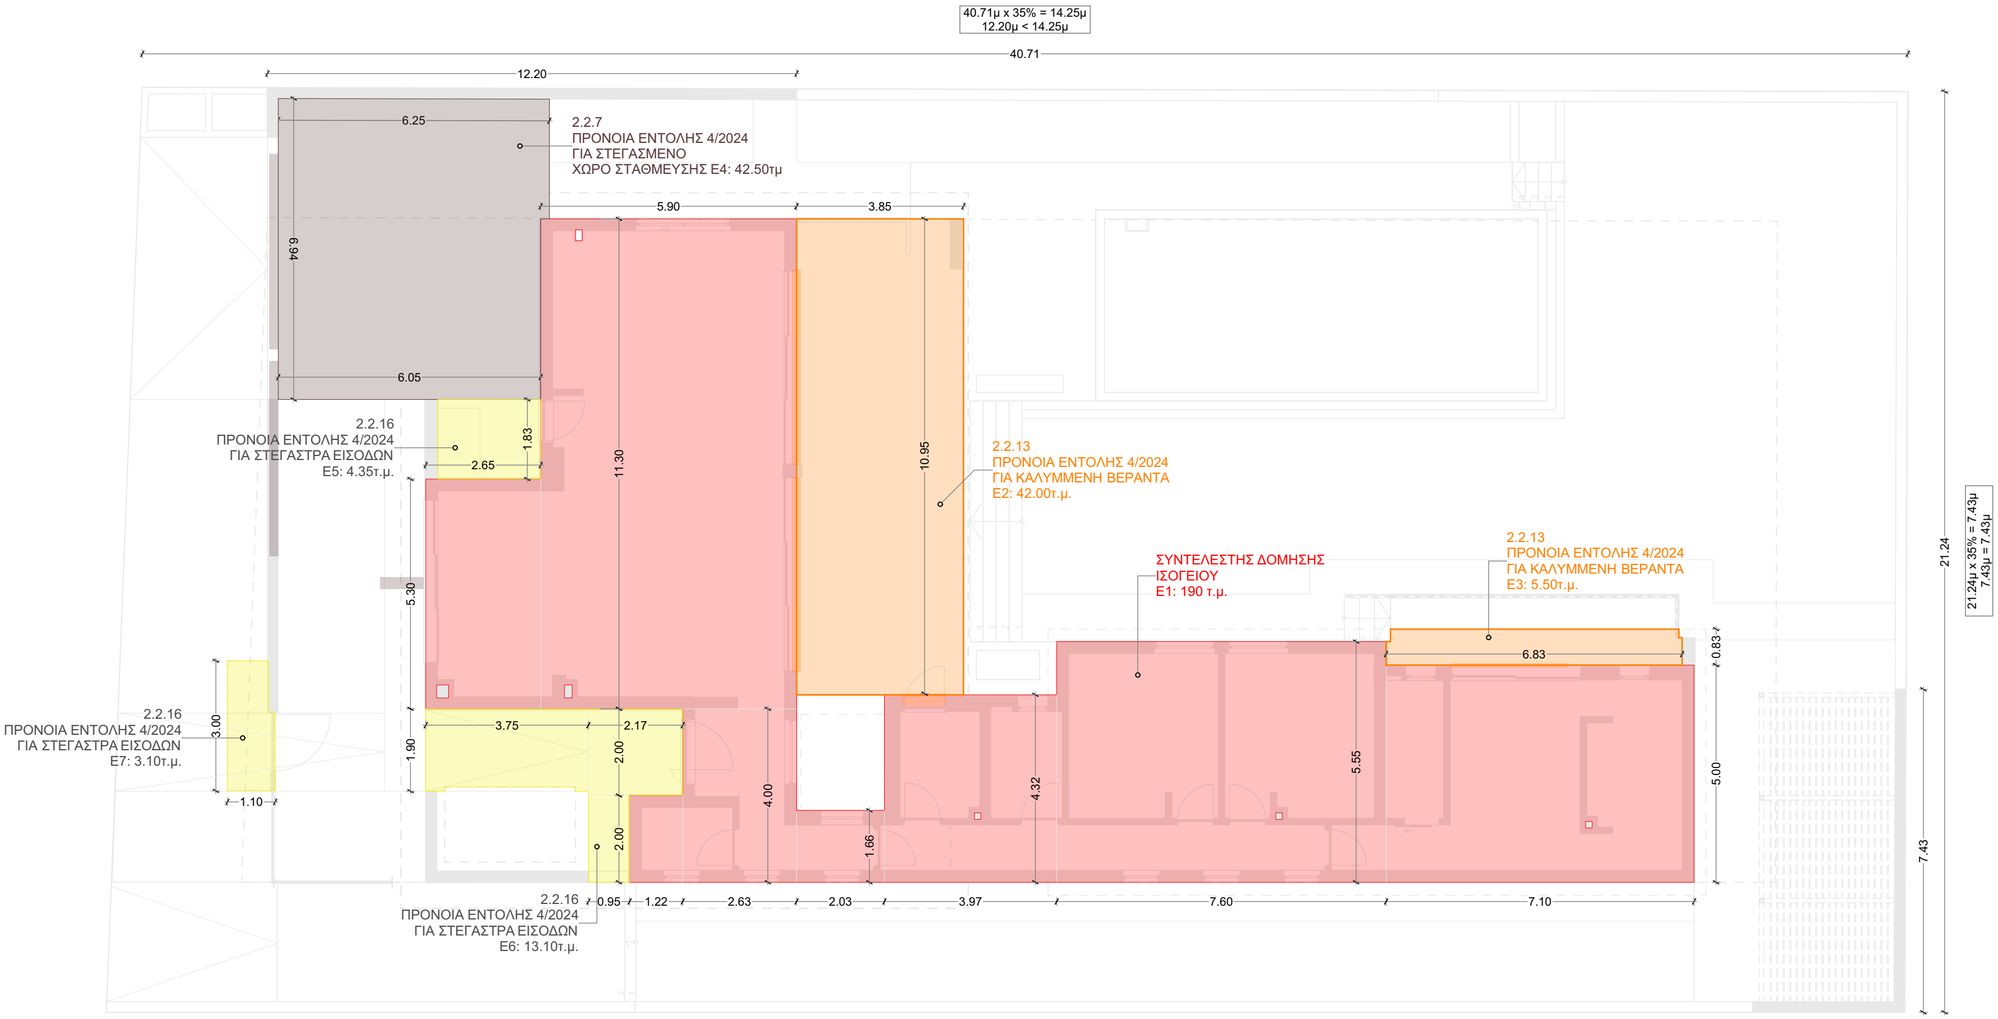

ΧΑΡΑΚΤΗΡΙΣΤΙΚΑ ΤΕΜΑΧΙΟΥ ΚΑΙ ΠΟΛΕΟΔΟΜΙΚΑ ΔΕΔΟΜΕΝΑ: ΕΓΓΕΓΡΑΜΜΕΝΟ ΩΣ ΟΙΚΟΠΕΔΟ ΤΜΗΜΑ/ΑΡ. ΕΓΓΡΑΦΗΣ: 6/2100 ΦΥΛΛΟ/ΣΧΕΔΙΟ: 30/23Ε2 ΑΡ. ΤΕΜΑΧΙΟΥ: 2021 ΔΗΜΟΣ: ΛΑΤΣΙΩΝ ΕΝΟΡΙΑ: ΑΓΙΟΣ ΓΕΩΡΓΙΟΣ ΠΟΛΕΟΔΟΜΙΚΗ ΖΩΝΗ: Κα6	ΠΡΟΤΕΙΝΟΜΕΝΟΣ Σ.Δ.: E1 190τμ / Εμβ. Τεμ. 877τμ = 21.6% < 90% ΠΡΟΤΕΙΝΟΜΕΝΟ Π.Κ.: Κ1 311.65τμ / Εμβ. Τεμ. 877τμ = 35.5% < 50%	**ΕΜΒΑΔΟ ΠΟΥ ΛΟΓΙΖΕΤΑΙ ΣΤΟΝ ΣΔ**		**ΕΜΒΑΔΟ ΠΟΥ ΛΟΓΙΖΕΤΑΙ ΣΤΟ ΠΚ**		**ΧΩΡΟΙ ΣΤΑΘΜΕΥΣΗΣ**
		ΔΟΜΗΣΙΜΟ ΕΜΒΑΔΟ (Ε1)	190τμ	ΚΑΛΥΜΜΕΝΟΙ ΧΩΡΟΙ (Κ1)	311.65τμ	ΑΠΑΙΤΟΜΕΝΟΙ: Σύμφωνα με την Εντολή 1/2016 παρ. 4.2 1(γ) για ωφέλιμο εμβαδόν: 190τμ (> 150τμ) απαιτούνται 2 χ.σ. ΠΡΟΤΕΙΝΟΜΕΝΟΙ: 3 χ.σ.
		ΣΥΝΟΛΟ Σ.Δ. ΠΟΥ ΛΟΓΙΖΕΤΑΙ	190τμ	ΣΥΝΟΛΟ Π.Κ. ΠΟΥ ΛΟΓΙΖΕΤΑΙ	311.65τμ	
		ΕΜΒΑΔΟ ΠΟΥ ΔΕΝ ΛΟΓΙΖΕΤΑΙ ΣΤΟΝ ΣΔ		**ΕΜΒΑΔΟ ΠΟΥ ΔΕΝ ΛΟΓΙΖΕΤΑΙ ΣΤΟ ΠΚ**		
ΕΠΙΤΡΕΠΟΜΕΝΟΣ Σ.Δ.: 0.9 ΕΠΙΤΡΕΠΟΜΕΝΟ Π.Κ.: 0.5 ΕΠΙΤΡΕΠΟΜΕΝΟΙ ΟΡΟΦΟΙ: 2 ΕΠΙΤΡΕΠΟΜΕΝΟ ΥΨΟΣ: 10μ.	ΠΡΟΤΕΙΝΟΜΕΝΟΙ ΟΡΟΦΟΙ: 1 ΠΡΟΤΕΙΝΟΜΕΝΟ ΥΨΟΣ: 5μ.	ΚΑΛΥΜΜΕΝΕΣ ΒΕΡΑΝΤΕΣ (Ε2 + Ε3)	47.5τμ	ΑΡΧΙΤΕΚΤΟΝΙΚΕΣ ΠΡΟΕΞΟΧΕΣ (Κ2, Κ3 & Κ4)	36τμ	
		ΣΤΕΓΑΣΜΕΝΟΣ ΧΩΡΟΣ ΣΤΑΘΜΕΥΣΗΣ (Ε4)	42.5τμ	ΣΤΕΓΑΣΤΡΟ ΕΙΣΟΔΟΥ (Κ5)	3.30τμ	
ΕΜΒΑΔΟ ΤΕΜΑΧΙΟΥ: 877τ.μ. ΕΠΙΤΡΕΠΟΜΕΝΟΣ Σ.Δ.: 0.9 x 877 = 789.3τμ ΕΠΙΤΡΕΠΟΜΕΝΟ Π.Κ.: 0.5 x 877 = 438.5τμ	ΠΡΟΤΕΙΝΟΜΕΝΕΣ ΚΑΛΥΜΜΕΝΕΣ ΒΕΡΑΝΤΕΣ: ΕΠΙΤΡΕΠΟΜΕΝΟ ΕΜΒΑΔΟ: 190τμ x 25% = 47.50τμ [2.2.13(α) ΕΝΤΟΛΗ 4/2024]	ΣΤΕΓΑΣΜΕΝΟΙ ΧΩΡΟΙ ΕΙΣΟΔΩΝ (Ε5 + Ε6 + Ε7)	20.55τμ	ΣΥΝΟΛΟ (ΔΕΝ ΛΟΓΙΖΕΤΑΙ)	39.30τμ	
ΣΤΟΙΧΕΙΑ ΕΡΓΟΥ: ΙΣΟΓΕΙΑ ΚΑΤΟΙΚΙΑ	ΣΥΝΟΛΙΚΟ ΕΜΒΑΔΟ ΚΑΛ. ΒΕΡΑΝΤΩΝ: Ε2 + Ε3 = 42.00 + 5.50 = 47.50τμ	ΣΥΝΟΛΟ (ΔΕΝ ΛΟΓΙΖΕΤΑΙ)	110.55τμ			

Υπόμνημα Υψομέτρων

— ±000.00 —	ΥΦΙΣΤΑΜΕΝΕΣ ΙΣΟΫΨΕΙΣ ΓΡΑΜΜΕΣ
±000.00	ΥΦΙΣΤΑΜΕΝΑ ΥΨΟΜΕΤΡΑ
±000.00	ΠΡΟΤΕΙΝΟΜΕΝΑ ΥΨΟΜΕΤΡΑ

±0.00μ. = +214μ. (ΠΡΑΓΜΑΤΙΚΟ ΥΨΟΜΕΤΡΟ)

Υπόμνημα Υλικών

1	Μπετόν Σανιδωτό
2	Οπτοπλινθοδομή / Σοβάς
3	Μπετόν / Σοβάς
4	Επένδυση Alucobond
5	Πλέγμα
6	Μεταλλική Πέργολα

Στοιχεία Τεμαχίου

ΤΜΗΜΑ/ΑΡ. ΕΓΓΡΑΦΗΣ: 6/2100
ΦΥΛΛΟ/ΣΧΕΔΙΟ: 30/23Ε2
ΑΡ. ΤΕΜΑΧΙΟΥ: 2021
ΔΗΜΟΣ: ΛΑΤΣΙΩΝ
ΕΝΟΡΙΑ: ΑΓΙΟΣ ΓΕΩΡΓΙΟΣ
ΠΟΛΕΟΔΟΜΙΚΗ ΖΩΝΗ: Κα6

ΕΓΓΕΓΡΑΜΜΕΝΟ ΩΣ ΟΙΚΟΠΕΔΟ

ΣΤΟΙΧΕΙΑ ΕΡΓΟΥ: ΙΣΟΓΕΙΑ ΚΑΤΟΙΚΙΑ
ΔΟΜΗΣΙΜΟ ΕΜΒΑΔΟΝ: 190.00τ.μ.

ΕΝΤΟΛΗ 2/2020
ΠΟΛΕΟΔΟΜΙΚΗ ΑΔΕΙΑ

ΕΥΣΤΑΘΙΟΣ ΛΕΥΚΑΤΗΣ
ΑΡΧΙΤΕΚΤΟΝΑΣ
Α.Μ.ΕΤΕΚ: Α173321

Revision History

RevID	Comment	Date

Αρχιτέκτονας / Architect

LEFKATIS STATHIS ARCHITECTURE

STATHIS LEFKATIS ARCHITECTURE

4, KOURIOU STREET, LATSIA, NICOSIA
CYPRUS, 2220
e-mail: efstathios.lefkatis@gmail.com
tel: 99841485

Κύριος Έργου / Client

ΑΝΤΡΕΑΣ & ΜΑΡΙΑ

Έργο / Project Name

ΙΣΟΓΕΙΑ ΚΑΤΟΙΚΙΑ


Τίτλος Σχεδίου / Drawing Name

ΕΜΒΑΔΟΜΕΤΡΗΣΕΙΣ - Σ.Δ.

Φάση / Design Phase	Μελέτη / Study
ΠΟΛΕΟΔΟΜΙΚΗ ΑΔΕΙΑ	**ΑΡΧΙΤΕΚΤΟΝΙΚΗ**
Checked by	Ημερομηνία / Date
ΣΤΑΘΗΣ ΛΕΥΚΑΤΗΣ	**20/03/2026**
Layout ID	Revision
A5.1	

Κλίμακα Σχεδίου / Drawing Scale

1:100 @ A2

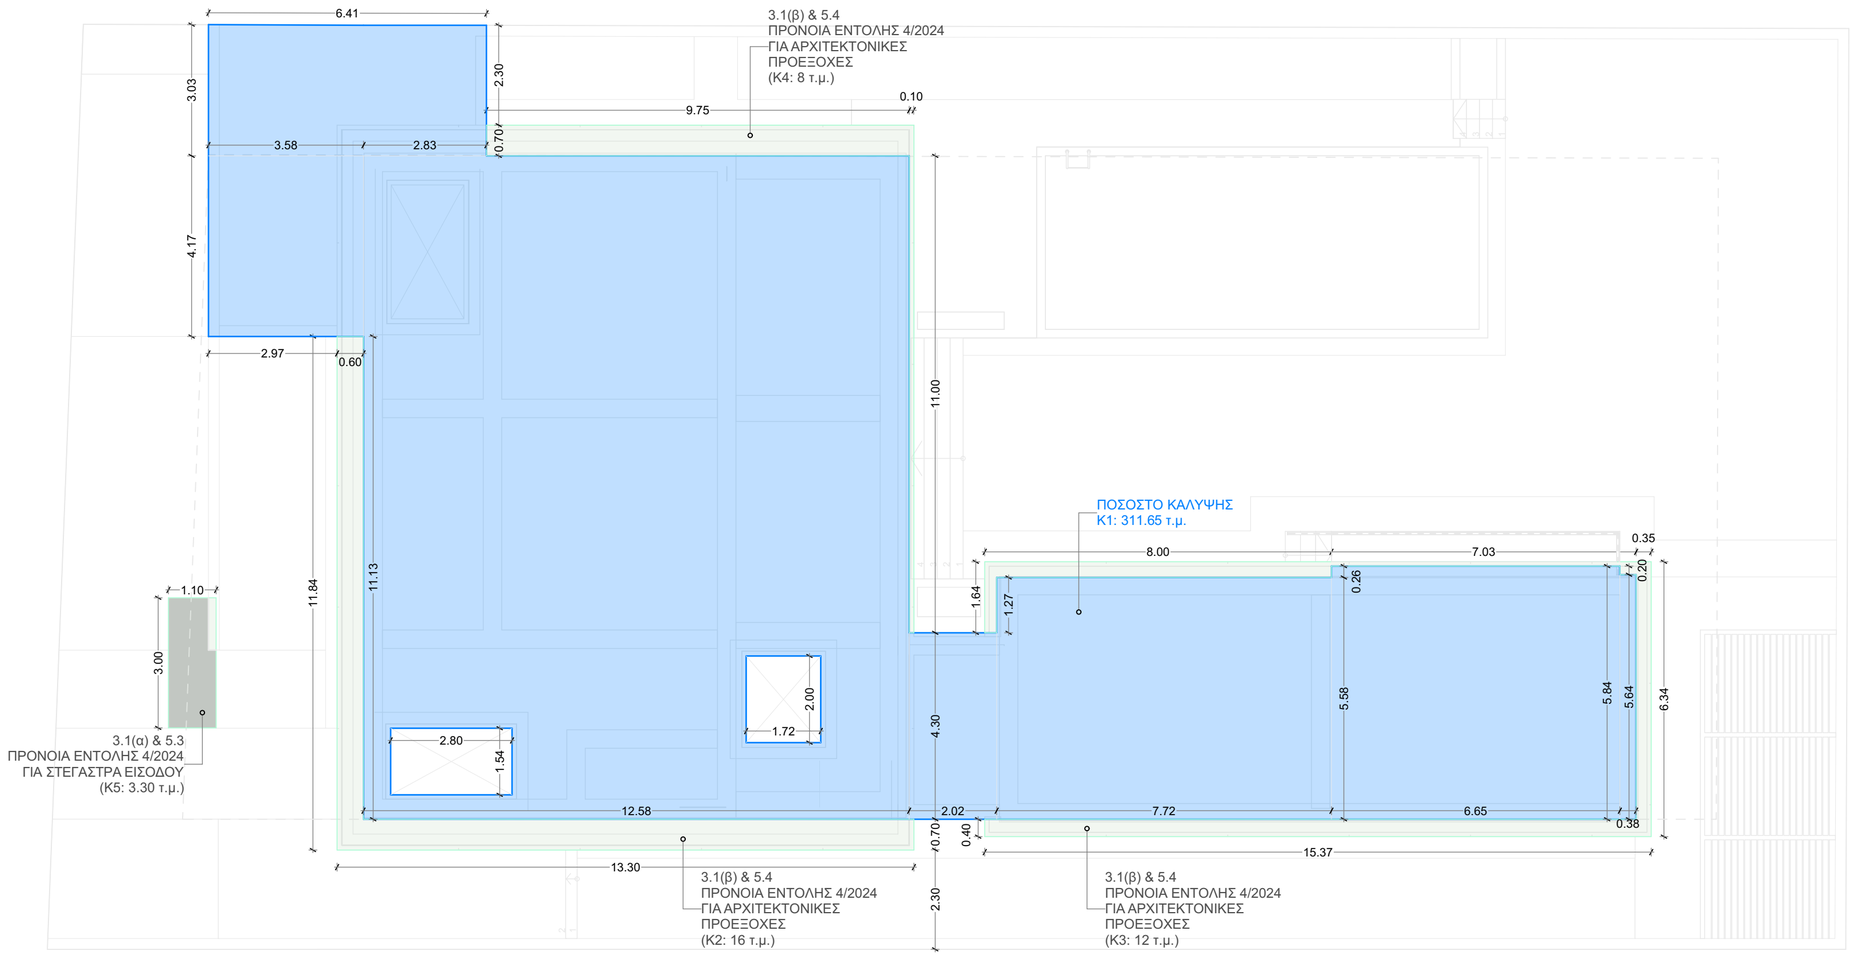

ΧΑΡΑΚΤΗΡΙΣΤΙΚΑ ΤΕΜΑΧΙΟΥ ΚΑΙ ΠΟΛΕΟΔΟΜΙΚΑ ΔΕΔΟΜΕΝΑ:		ΕΜΒΑΔΟ ΠΟΥ ΛΟΓΙΖΕΤΑΙ ΣΤΟΝ ΣΔ		ΕΜΒΑΔΟ ΠΟΥ ΛΟΓΙΖΕΤΑΙ ΣΤΟ ΠΚ		ΧΩΡΟΙ ΣΤΑΘΜΕΥΣΗΣ
ΕΓΓΕΓΡΑΜΜΕΝΟ ΩΣ ΟΙΚΟΠΕΔΟ ΤΜΗΜΑ/ΑΡ. ΕΓΓΡΑΦΗΣ: 6/2100 ΦΥΛΛΟ/ΣΧΕΔΙΟ: 30/23Ε2 ΑΡ. ΤΕΜΑΧΙΟΥ: 2021 ΔΗΜΟΣ: ΛΑΤΣΙΩΝ ΕΝΟΡΙΑ: ΑΓΙΟΣ ΓΕΩΡΓΙΟΣ ΠΟΛΕΟΔΟΜΙΚΗ ΖΩΝΗ: Κα6	ΠΡΟΤΕΙΝΟΜΕΝΟΣ Σ.Δ.: Ε1 / Εμβ. Τεμ. = 190τμ / 877τμ = 21.6% < 90% ΠΡΟΤΕΙΝΟΜΕΝΟ Π.Κ.: Κ1 / Εμβ. Τεμ. = 311.65τμ / 877τμ = 35.5% < 50%	ΔΟΜΗΣΙΜΟ ΕΜΒΑΔΟ (Ε1)	190τμ	ΚΑΛΥΜΜΕΝΟΙ ΧΩΡΟΙ (Κ1)	311.65τμ	ΑΠΑΙΤΟΜΕΝΟΙ: Σύμφωνα με την Εντολή 1/2016 παρ. 4.2 1(γ) για ωφέλιμο εμβαδόν: 190τμ (> 150τμ) απαιτούνται 2 χ.σ. ΠΡΟΤΕΙΝΟΜΕΝΟΙ: 3 χ.σ.
		ΣΥΝΟΛΟ Σ.Δ. ΠΟΥ ΛΟΓΙΖΕΤΑΙ	190τμ	ΣΥΝΟΛΟ Π.Κ. ΠΟΥ ΛΟΓΙΖΕΤΑΙ	311.65τμ	
		ΕΜΒΑΔΟ ΠΟΥ ΔΕΝ ΛΟΓΙΖΕΤΑΙ ΣΤΟΝ ΣΔ		**ΕΜΒΑΔΟ ΠΟΥ ΔΕΝ ΛΟΓΙΖΕΤΑΙ ΣΤΟ ΠΚ**		
ΕΠΙΤΡΕΠΟΜΕΝΟΣ Σ.Δ.: 0.9 ΕΠΙΤΡΕΠΟΜΕΝΟ Π.Κ.: 0.5 ΕΠΙΤΡΕΠΟΜΕΝΟΙ ΟΡΟΦΟΙ: 2 ΕΠΙΤΡΕΠΟΜΕΝΟ ΥΨΟΣ: 10μ.	ΠΡΟΤΕΙΝΟΜΕΝΟΙ ΟΡΟΦΟΙ: 1 ΠΡΟΤΕΙΝΟΜΕΝΟ ΥΨΟΣ: 5μ.	ΚΑΛΥΜΜΕΝΕΣ ΒΕΡΑΝΤΕΣ (Ε2 + Ε3)	47.5τμ	ΑΡΧΙΤΕΚΤΟΝΙΚΕΣ ΠΡΟΕΞΟΧΕΣ (Κ2, Κ3 & Κ4)	36τμ	
		ΣΤΕΓΑΣΜΕΝΟΣ ΧΩΡΟΣ ΣΤΑΘΜΕΥΣΗΣ (Ε4)	42.5τμ	ΣΤΕΓΑΣΤΡΟ ΕΙΣΟΔΟΥ (Κ5)	3.30τμ	
ΕΜΒΑΔΟ ΤΕΜΑΧΙΟΥ: 877τ.μ. ΕΠΙΤΡΕΠΟΜΕΝΟΣ Σ.Δ.: 0.9 x 877 = 789.3τμ ΕΠΙΤΡΕΠΟΜΕΝΟ Π.Κ.: 0.5 x 877 = 438.5τμ	ΠΡΟΤΕΙΝΟΜΕΝΕΣ ΚΑΛΥΜΜΕΝΕΣ ΒΕΡΑΝΤΕΣ: ΕΠΙΤΡΕΠΟΜΕΝΟ ΕΜΒΑΔΟ: 190τμ x 25% = 47.50τμ [2.2.13(α) ΕΝΤΟΛΗ 4/2024]	ΣΤΕΓΑΣΜΕΝΟΙ ΧΩΡΟΙ ΕΙΣΟΔΩΝ (Ε5 + Ε6 + Ε7)	20.55τμ	ΣΥΝΟΛΟ (ΔΕΝ ΛΟΓΙΖΕΤΑΙ)	39.30τμ	
		ΣΥΝΟΛΟ (ΔΕΝ ΛΟΓΙΖΕΤΑΙ)	110.55τμ			
ΣΤΟΙΧΕΙΑ ΕΡΓΟΥ: ΙΣΟΓΕΙΑ ΚΑΤΟΙΚΙΑ	ΣΥΝΟΛΙΚΟ ΕΜΒΑΔΟ ΚΑΛ. ΒΕΡΑΝΤΩΝ: Ε2 + Ε3 = 42.00 + 5.50 = 47.50τμ					

Υπόμνημα Υψομέτρων

— ±000.00 — ΥΦΙΣΤΑΜΕΝΕΣ ΙΣΟΫΨΕΙΣ ΓΡΑΜΜΕΣ

±000.00 ΥΦΙΣΤΑΜΕΝΑ ΥΨΟΜΕΤΡΑ

±000.00 ΠΡΟΤΕΙΝΟΜΕΝΑ ΥΨΟΜΕΤΡΑ

±0.00μ. = +214μ. (ΠΡΑΓΜΑΤΙΚΟ ΥΨΟΜΕΤΡΟ)

Υπόμνημα Υλικών

1 Μπετόν Σανιδωτό

2 Οπτοπλινθοδομή / Σοβάς

3 Μπετόν / Σοβάς

4 Επένδυση Alucobond

5 Πλέγμα

6 Μεταλλική Πέργολα

Στοιχεία Τεμαχίου

ΤΜΗΜΑ/ΑΡ. ΕΓΓΡΑΦΗΣ: 6/2100
ΦΥΛΛΟ/ΣΧΕΔΙΟ: 30/23Ε2
ΑΡ. ΤΕΜΑΧΙΟΥ: 2021
ΔΗΜΟΣ: ΛΑΤΣΙΩΝ
ΕΝΟΡΙΑ: ΑΓΙΟΣ ΓΕΩΡΓΙΟΣ
ΠΟΛΕΟΔΟΜΙΚΗ ΖΩΝΗ: Κα6

ΕΓΓΕΓΡΑΜΜΕΝΟ ΩΣ ΟΙΚΟΠΕΔΟ

ΣΤΟΙΧΕΙΑ ΕΡΓΟΥ: ΙΣΟΓΕΙΑ ΚΑΤΟΙΚΙΑ
ΔΟΜΗΣΙΜΟ ΕΜΒΑΔΟΝ: 190.00τ.μ.

ΕΝΤΟΛΗ 2/2020
ΠΟΛΕΟΔΟΜΙΚΗ ΑΔΕΙΑ

ΕΥΣΤΑΘΙΟΣ ΛΕΥΚΑΤΗΣ
ΑΡΧΙΤΕΚΤΟΝΑΣ
Α.Μ.ΕΤΕΚ: Α173321

Revision History

RevID	Comment	Date

Αρχιτέκτονας / Architect

LEFKATIS STATHIS ARCHITECTURE

STATHIS LEFKATIS ARCHITECTURE

4, KOURIOU STREET, LATSIA, NICOSIA
CYPRUS, 2220
e-mail: efstathios.lefkatis@gmail.com
tel: 99841485

Κύριος Έργου / Client

ΑΝΤΡΕΑΣ & ΜΑΡΙΑ

Έργο / Project Name

ΙΣΟΓΕΙΑ ΚΑΤΟΙΚΙΑ

Τίτλος Σχεδίου / Drawing Name

ΕΜΒΑΔΟΜΕΤΡΗΣΕΙΣ - Π.Κ.

Φάση / Design Phase	Μελέτη / Study
ΠΟΛΕΟΔΟΜΙΚΗ ΑΔΕΙΑ	**ΑΡΧΙΤΕΚΤΟΝΙΚΗ**
Checked by	Ημερομηνία / Date
ΣΤΑΘΗΣ ΛΕΥΚΑΤΗΣ	**20/03/2026**


Layout ID **A5.2** Revision

Κλίμακα Σχεδίου / Drawing Scale

1:100 @ A2





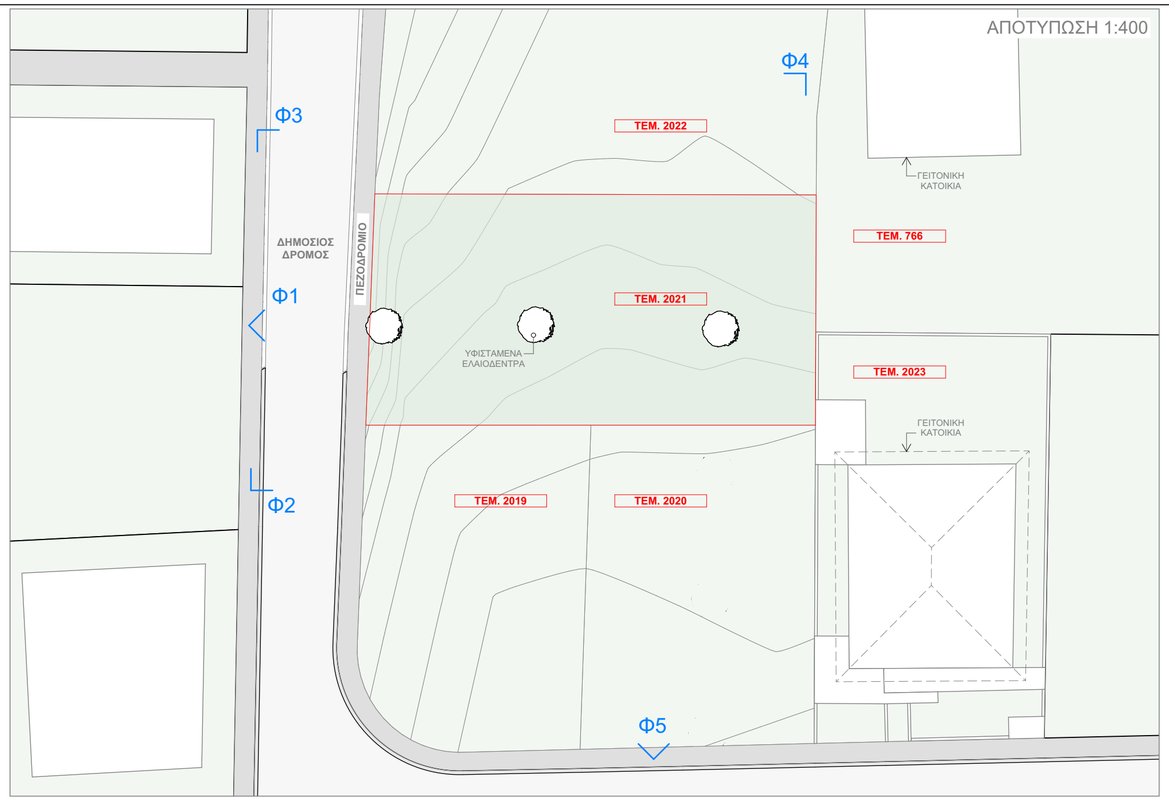









Υπόμνημα Υψομέτρων

— ±000.00 —	ΥΦΙΣΤΑΜΕΝΕΣ ΙΣΟΫΨΕΙΣ ΓΡΑΜΜΕΣ
±000.00	ΥΦΙΣΤΑΜΕΝΑ ΥΨΟΜΕΤΡΑ
±000.00	ΠΡΟΤΕΙΝΟΜΕΝΑ ΥΨΟΜΕΤΡΑ

±0.00μ. = +214μ. (ΠΡΑΓΜΑΤΙΚΟ ΥΨΟΜΕΤΡΟ)

Υπόμνημα Υλικών

1	Μπετόν Σανιδωτό
2	Οπτοπλινθοδομή / Σοβάς
3	Μπετόν / Σοβάς
4	Επένδυση Alucobond
5	Πλέγμα
6	Μεταλλική Πέργολα

Στοιχεία Τεμαχίου

ΤΜΗΜΑ/ΑΡ. ΕΓΓΡΑΦΗΣ: 6/2100
ΦΥΛΛΟ/ΣΧΕΔΙΟ: 30/23E2
ΑΡ. ΤΕΜΑΧΙΟΥ: 2021
ΔΗΜΟΣ: ΛΑΤΣΙΩΝ
ΕΝΟΡΙΑ: ΑΓΙΟΣ ΓΕΩΡΓΙΟΣ
ΠΟΛΕΟΔΟΜΙΚΗ ΖΩΝΗ: Κα6

ΕΓΓΕΓΡΑΜΜΕΝΟ ΩΣ ΟΙΚΟΠΕΔΟ

ΣΤΟΙΧΕΙΑ ΕΡΓΟΥ: ΙΣΟΓΕΙΑ ΚΑΤΟΙΚΙΑ
ΔΟΜΗΣΙΜΟ ΕΜΒΑΔΟΝ: 190.00τ.μ.

ΕΝΤΟΛΗ 2/2020
ΠΟΛΕΟΔΟΜΙΚΗ ΑΔΕΙΑ

ΕΥΣΤΑΘΙΟΣ ΛΕΥΚΑΤΗΣ
ΑΡΧΙΤΕΚΤΟΝΑΣ
Α.Μ.ΕΤΕΚ: Α173321

Revision History

RevID	Comment	Date

Αρχιτέκτονας / Architect

LEFKATIS STATHIS ARCHITECTURE

STATHIS LEFKATIS ARCHITECTURE

4, KOURIOU STREET, LATSIA, NICOSIA
CYPRUS, 2220
e-mail: efstathios.lefkatis@gmail.com
tel: 99841485

Κύριος Έργου / Client

ΑΝΤΡΕΑΣ & ΜΑΡΙΑ

Έργο / Project Name

ΙΣΟΓΕΙΑ ΚΑΤΟΙΚΙΑ

Τίτλος Σχεδίου / Drawing Name

ΦΩΤΟΓΡΑΦΙΕΣ

Φάση / Design Phase	Μελέτη / Study
ΠΟΛΕΟΔΟΜΙΚΗ ΑΔΕΙΑ	**ΑΡΧΙΤΕΚΤΟΝΙΚΗ**
Checked by	Ημερομηνία / Date
ΣΤΑΘΗΣ ΛΕΥΚΑΤΗΣ	**20/03/2026**
Layout ID	Revision
A6	

Κλίμακα Σχεδίου / Drawing Scale

1:400 @ A2