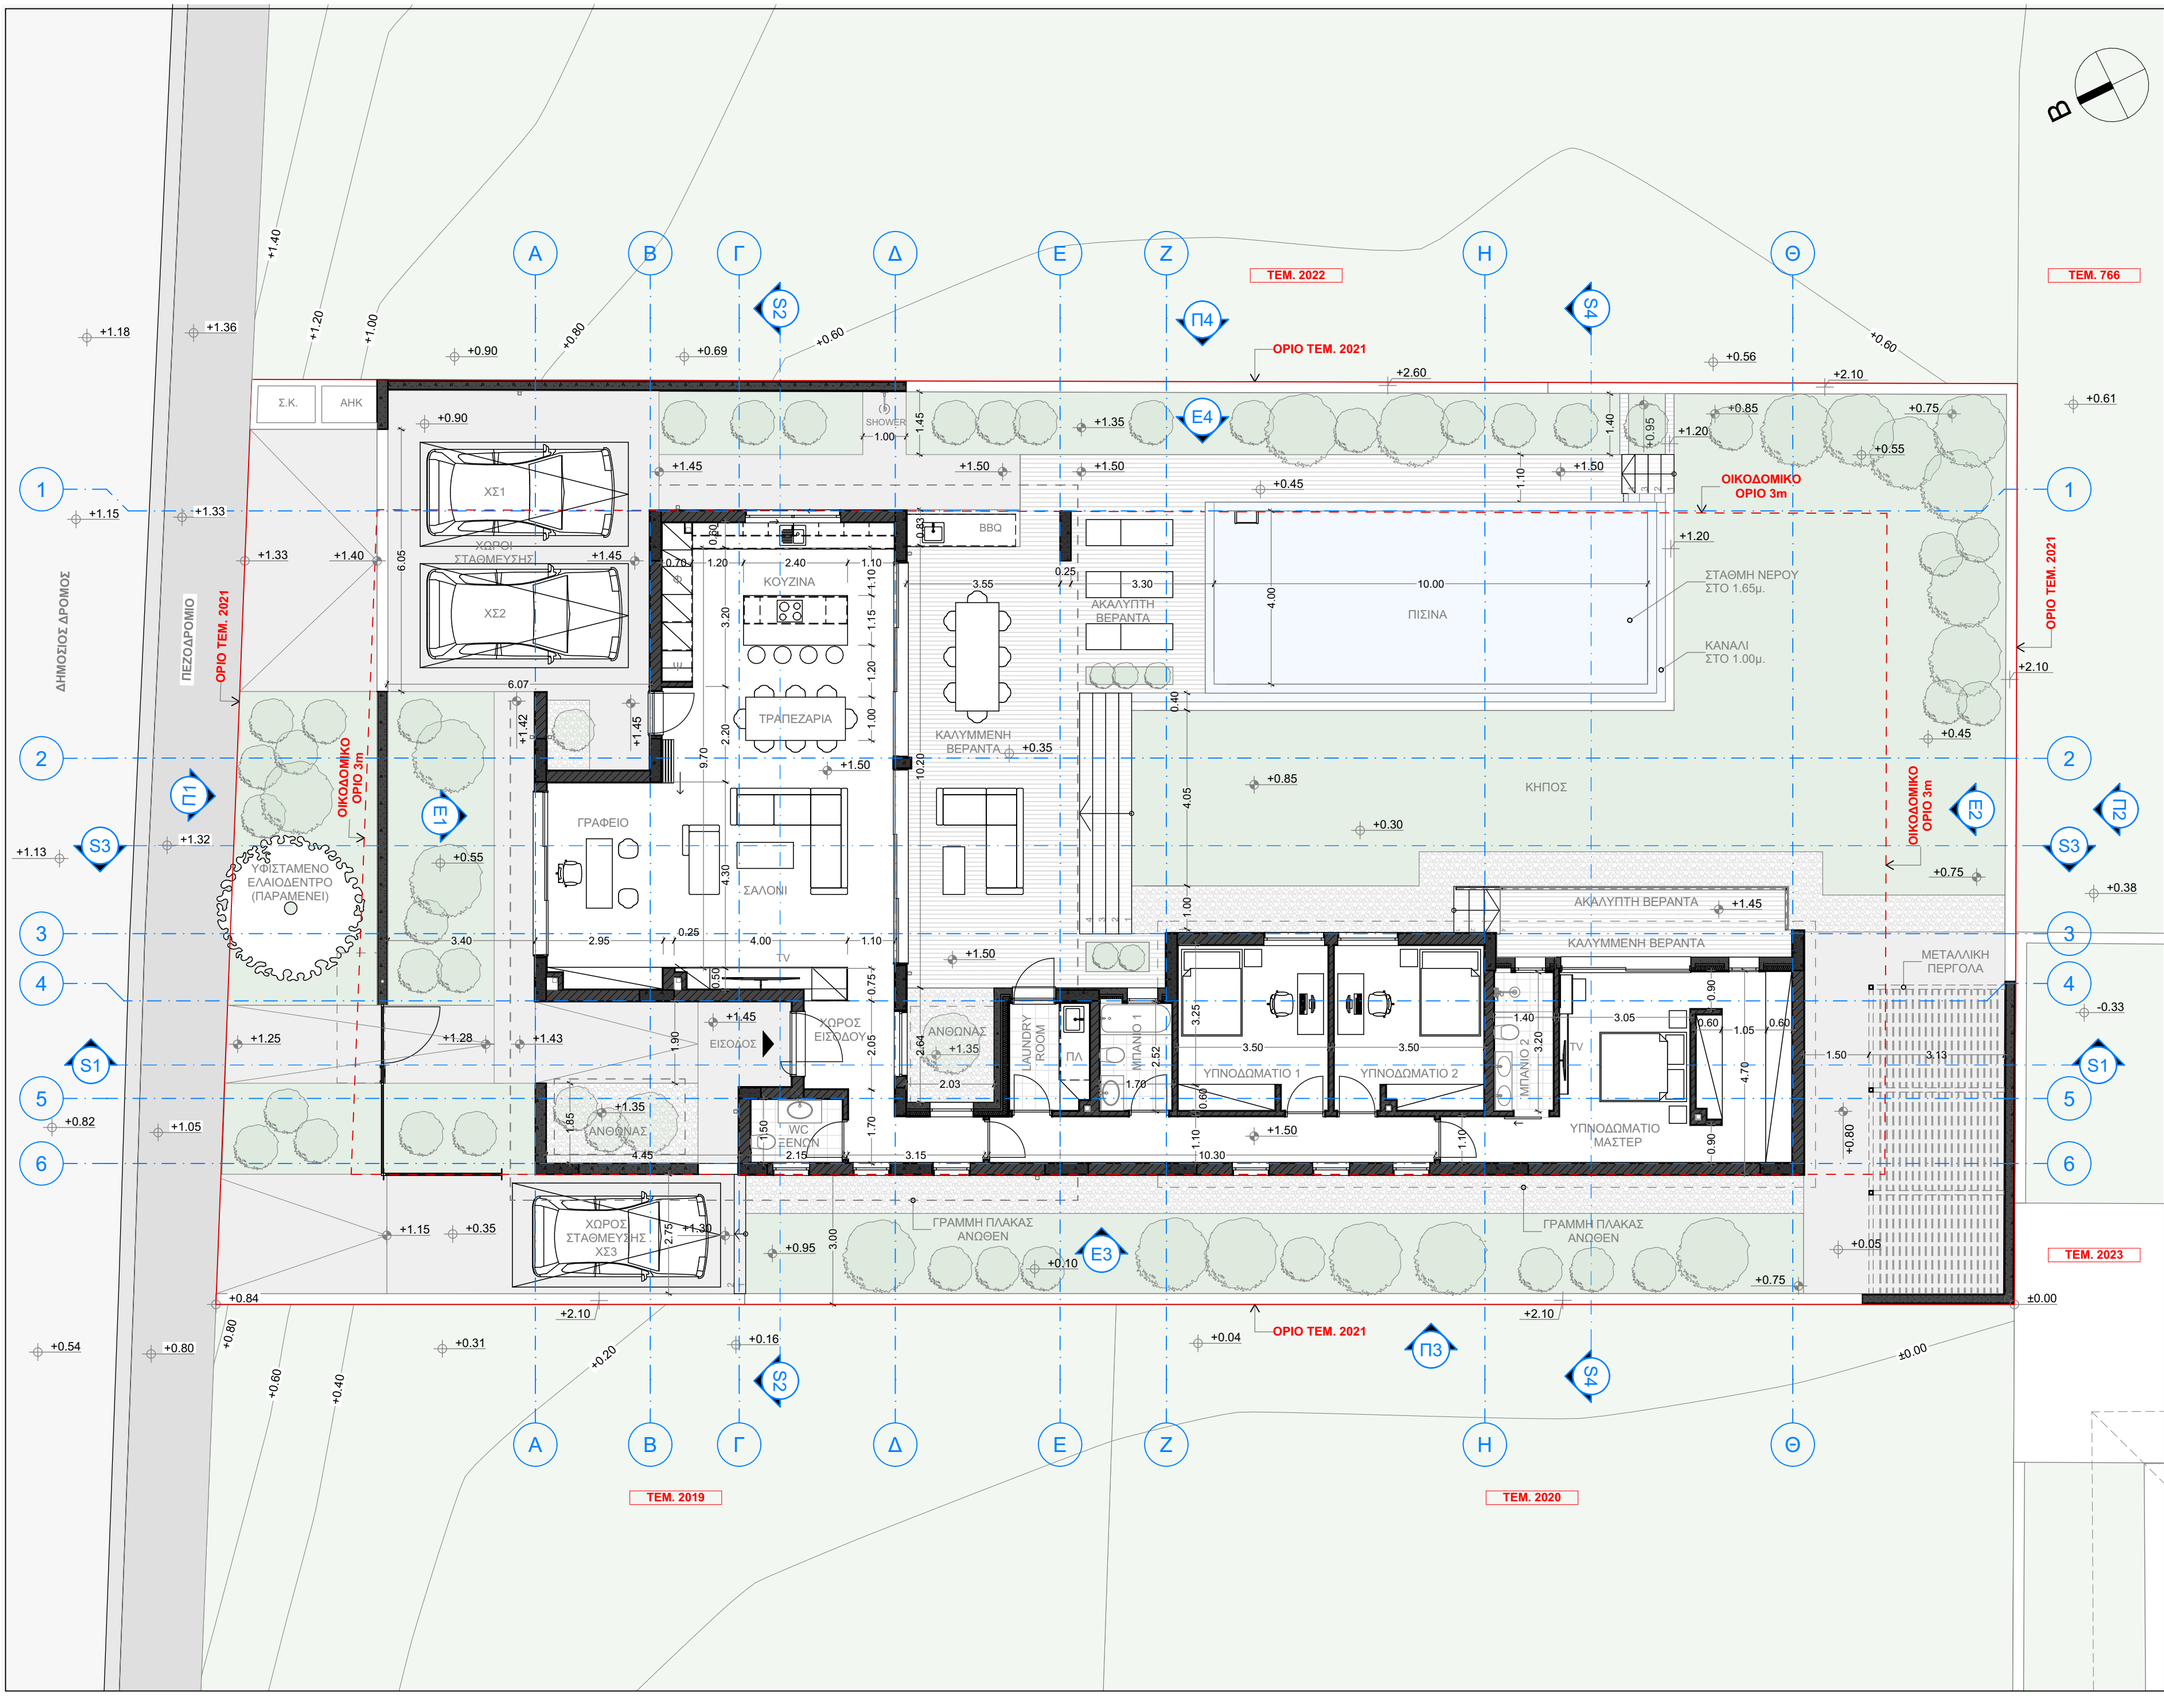


Υπόμνημα Υψομέτρων

— ±000.00 —	ΥΦΙΣΤΑΜΕΝΕΣ ΙΣΟΫΨΕΙΣ ΓΡΑΜΜΕΣ
±000.00	ΥΦΙΣΤΑΜΕΝΑ ΥΨΟΜΕΤΡΑ
±000.00	ΠΡΟΤΕΙΝΟΜΕΝΑ ΥΨΟΜΕΤΡΑ

±0.00μ. = +214μ. (ΠΡΑΓΜΑΤΙΚΟ ΥΨΟΜΕΤΡΟ)

Υπόμνημα Υλικών

1	Μπετόν Σανιδωτό
2	Οπτοπλινθοδομή / Σοβάς
3	Μπετόν / Σοβάς
4	Επένδυση Alucobond
5	Πλέγμα
6	Μεταλλική Πέργολα

Στοιχεία Τεμαχίου

ΤΜΗΜΑ/ΑΡ. ΕΓΓΡΑΦΗΣ: 6/2100
ΦΥΛΛΟ/ΣΧΕΔΙΟ: 30/23Ε2
ΑΡ. ΤΕΜΑΧΙΟΥ: 2021
ΔΗΜΟΣ: ΛΑΤΣΙΩΝ
ΕΝΟΡΙΑ: ΑΓΙΟΣ ΓΕΩΡΓΙΟΣ
ΠΟΛΕΟΔΟΜΙΚΗ ΖΩΝΗ: Κα6

ΕΓΓΕΓΡΑΜΜΕΝΟ ΩΣ ΟΙΚΟΠΕΔΟ

ΣΤΟΙΧΕΙΑ ΕΡΓΟΥ: ΙΣΟΓΕΙΑ ΚΑΤΟΙΚΙΑ
ΔΟΜΗΣΙΜΟ ΕΜΒΑΔΟΝ: 190.00τ.μ.

ΕΝΤΟΛΗ 2/2020
ΠΟΛΕΟΔΟΜΙΚΗ ΑΔΕΙΑ

ΕΥΣΤΑΘΙΟΣ ΛΕΥΚΑΤΗΣ
ΑΡΧΙΤΕΚΤΟΝΑΣ
Α.Μ.ΕΤΕΚ: Α173321

Revision History

RevID	Comment	Date

Αρχιτέκτονας / Architect

LEFKATIS STATHIS ARCHITECTURE

STATHIS LEFKATIS ARCHITECTURE

4, KOURIOU STREET, LATSIA, NICOSIA
CYPRUS, 2220
e-mail: efstathios.lefkatis@gmail.com
tel: 99841485

Κύριος Έργου / Client

ΑΝΤΡΕΑΣ & ΜΑΡΙΑ

Έργο / Project Name

ΙΣΟΓΕΙΑ ΚΑΤΟΙΚΙΑ

Τίτλος Σχεδίου / Drawing Name

ΚΑΤΟΨΗ ΙΣΟΓΕΙΟΥ

Φάση / Design Phase	Μελέτη / Study
ΠΟΛΕΟΔΟΜΙΚΗ ΑΔΕΙΑ	**ΑΡΧΙΤΕΚΤΟΝΙΚΗ**
Checked by	Ημερομηνία / Date
ΣΤΑΘΗΣ ΛΕΥΚΑΤΗΣ	**19/03/2026**
Layout ID	Revision
A1.2	

Κλίμακα Σχεδίου / Drawing Scale

1:100 @ A2