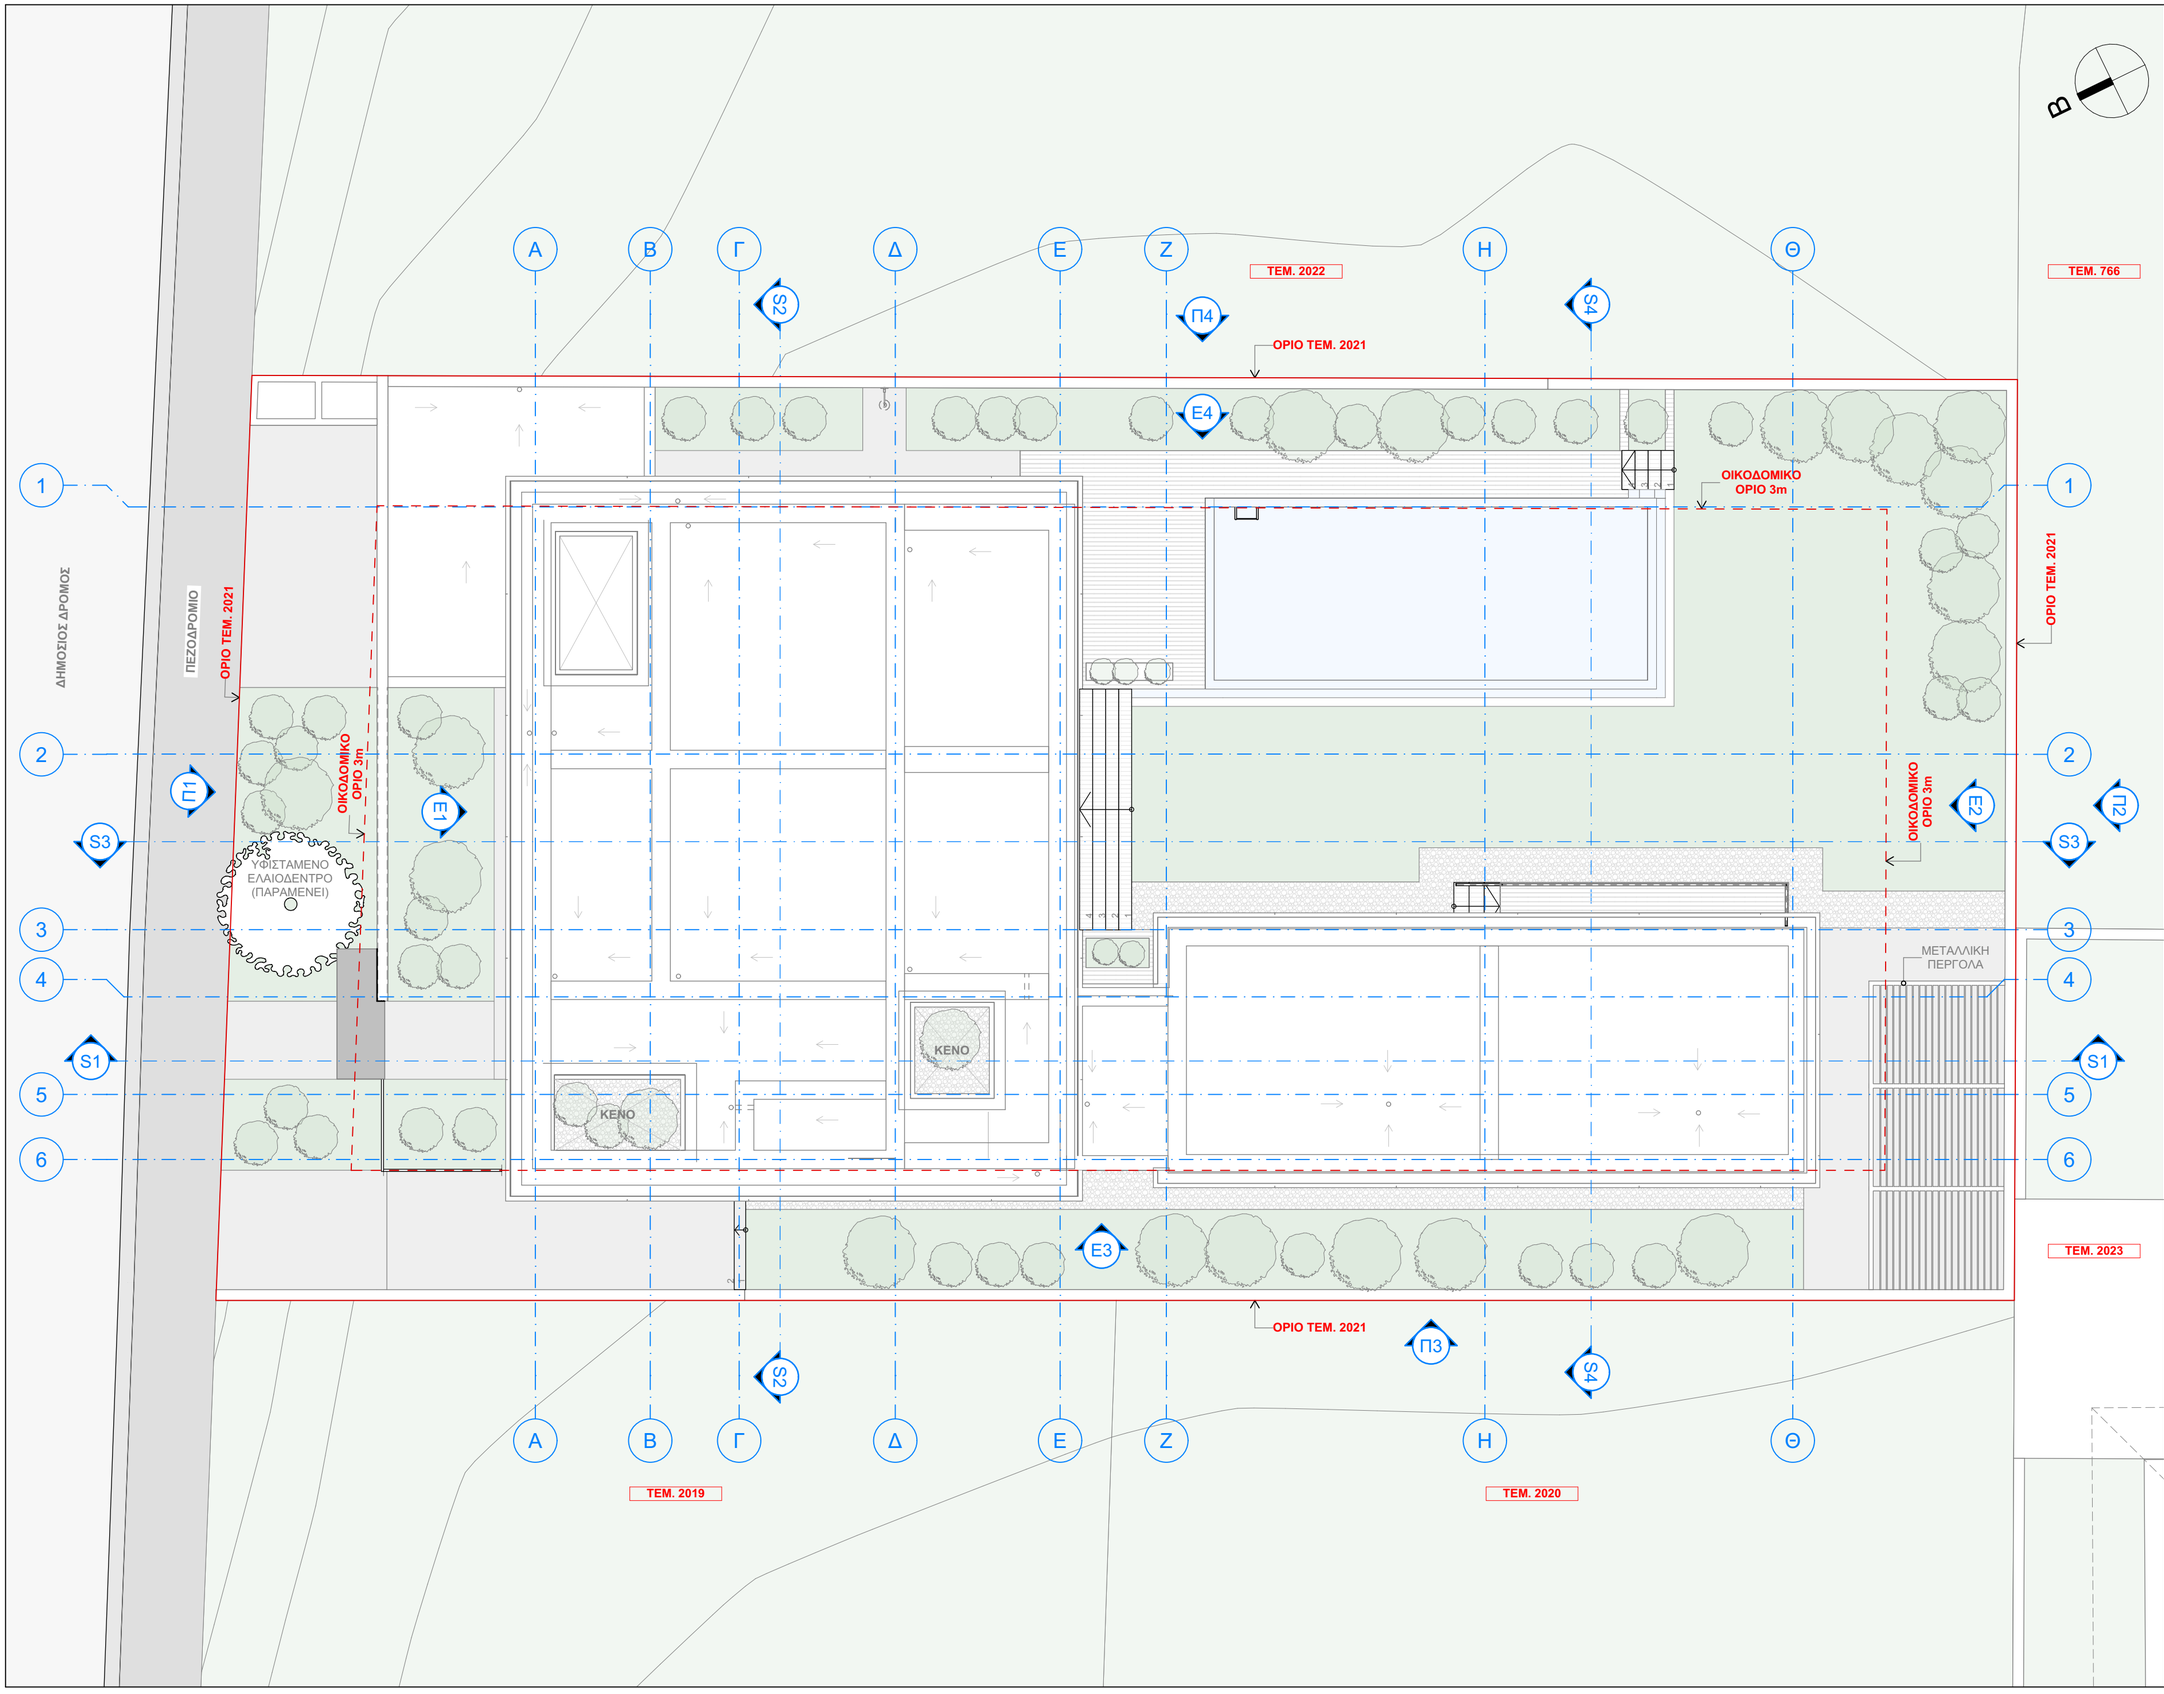



## Υπόμνημα Υψομέτρων

| | |
|---|---|
| — ±000.00 — | ΥΦΙΣΤΑΜΕΝΕΣ ΙΣΟΫΨΕΙΣ ΓΡΑΜΜΕΣ |
| ±000.00 | ΥΦΙΣΤΑΜΕΝΑ ΥΨΟΜΕΤΡΑ |
| ±000.00 | ΠΡΟΤΕΙΝΟΜΕΝΑ ΥΨΟΜΕΤΡΑ |

**±0.00μ. = +214μ. (ΠΡΑΓΜΑΤΙΚΟ ΥΨΟΜΕΤΡΟ)**

## Υπόμνημα Υλικών

| | |
|---|---|
| 1 | Μπετόν Σανιδωτό |
| 2 | Οπτοπλινθοδομή / Σοβάς |
| 3 | Μπετόν / Σοβάς |
| 4 | Επένδυση Alucobond |
| 5 | Πλέγμα |
| 6 | Μεταλλική Πέργολα |

## Στοιχεία Τεμαχίου

ΤΜΗΜΑ/ΑΡ. ΕΓΓΡΑΦΗΣ: 6/2100
ΦΥΛΛΟ/ΣΧΕΔΙΟ: 30/23Ε2
ΑΡ. ΤΕΜΑΧΙΟΥ: 2021
ΔΗΜΟΣ: ΛΑΤΣΙΩΝ
ΕΝΟΡΙΑ: ΑΓΙΟΣ ΓΕΩΡΓΙΟΣ
ΠΟΛΕΟΔΟΜΙΚΗ ΖΩΝΗ: Κα6

**ΕΓΓΕΓΡΑΜΜΕΝΟ ΩΣ ΟΙΚΟΠΕΔΟ**

ΣΤΟΙΧΕΙΑ ΕΡΓΟΥ: ΙΣΟΓΕΙΑ ΚΑΤΟΙΚΙΑ
ΔΟΜΗΣΙΜΟ ΕΜΒΑΔΟΝ: 190.00τ.μ.

**ΕΝΤΟΛΗ 2/2020**
**ΠΟΛΕΟΔΟΜΙΚΗ ΑΔΕΙΑ**


**ΕΥΣΤΑΘΙΟΣ ΛΕΥΚΑΤΗΣ**
**ΑΡΧΙΤΕΚΤΟΝΑΣ**
**Α.Μ.ΕΤΕΚ: Α173321**


Revision History

| RevID | Comment | Date |
|---|---|---|
| | | |


Αρχιτέκτονας / Architect

LEFKATIS STATHIS ARCHITECTURE

**STATHIS LEFKATIS ARCHITECTURE**

4, KOURIOU STREET, LATSIA, NICOSIA
CYPRUS, 2220
e-mail: efstathios.lefkatis@gmail.com
tel: 99841485


Κύριος Έργου / Client

**ΑΝΤΡΕΑΣ & ΜΑΡΙΑ**

Έργο / Project Name

**ΙΣΟΓΕΙΑ ΚΑΤΟΙΚΙΑ**

Τίτλος Σχεδίου / Drawing Name

**ΚΑΤΟΨΗ ΟΡΟΦΗΣ**

| Φάση / Design Phase | Μελέτη / Study |
|---|---|
| **ΠΟΛΕΟΔΟΜΙΚΗ ΑΔΕΙΑ** | **ΑΡΧΙΤΕΚΤΟΝΙΚΗ** |
| Checked by | Ημερομηνία / Date |
| **ΣΤΑΘΗΣ ΛΕΥΚΑΤΗΣ** | **19/03/2026** |
| Layout ID | Revision |
| **A1.3** | |

Κλίμακα Σχεδίου / Drawing Scale

**1:100 @ A2**